



TECH 101 LLC

N. Nawari, P.E.


Address:
1210 NW 106th ST
Gainesville, FL 32606
Phone: 303- 573- 6640
e-mail Nnawari1@gmail.com

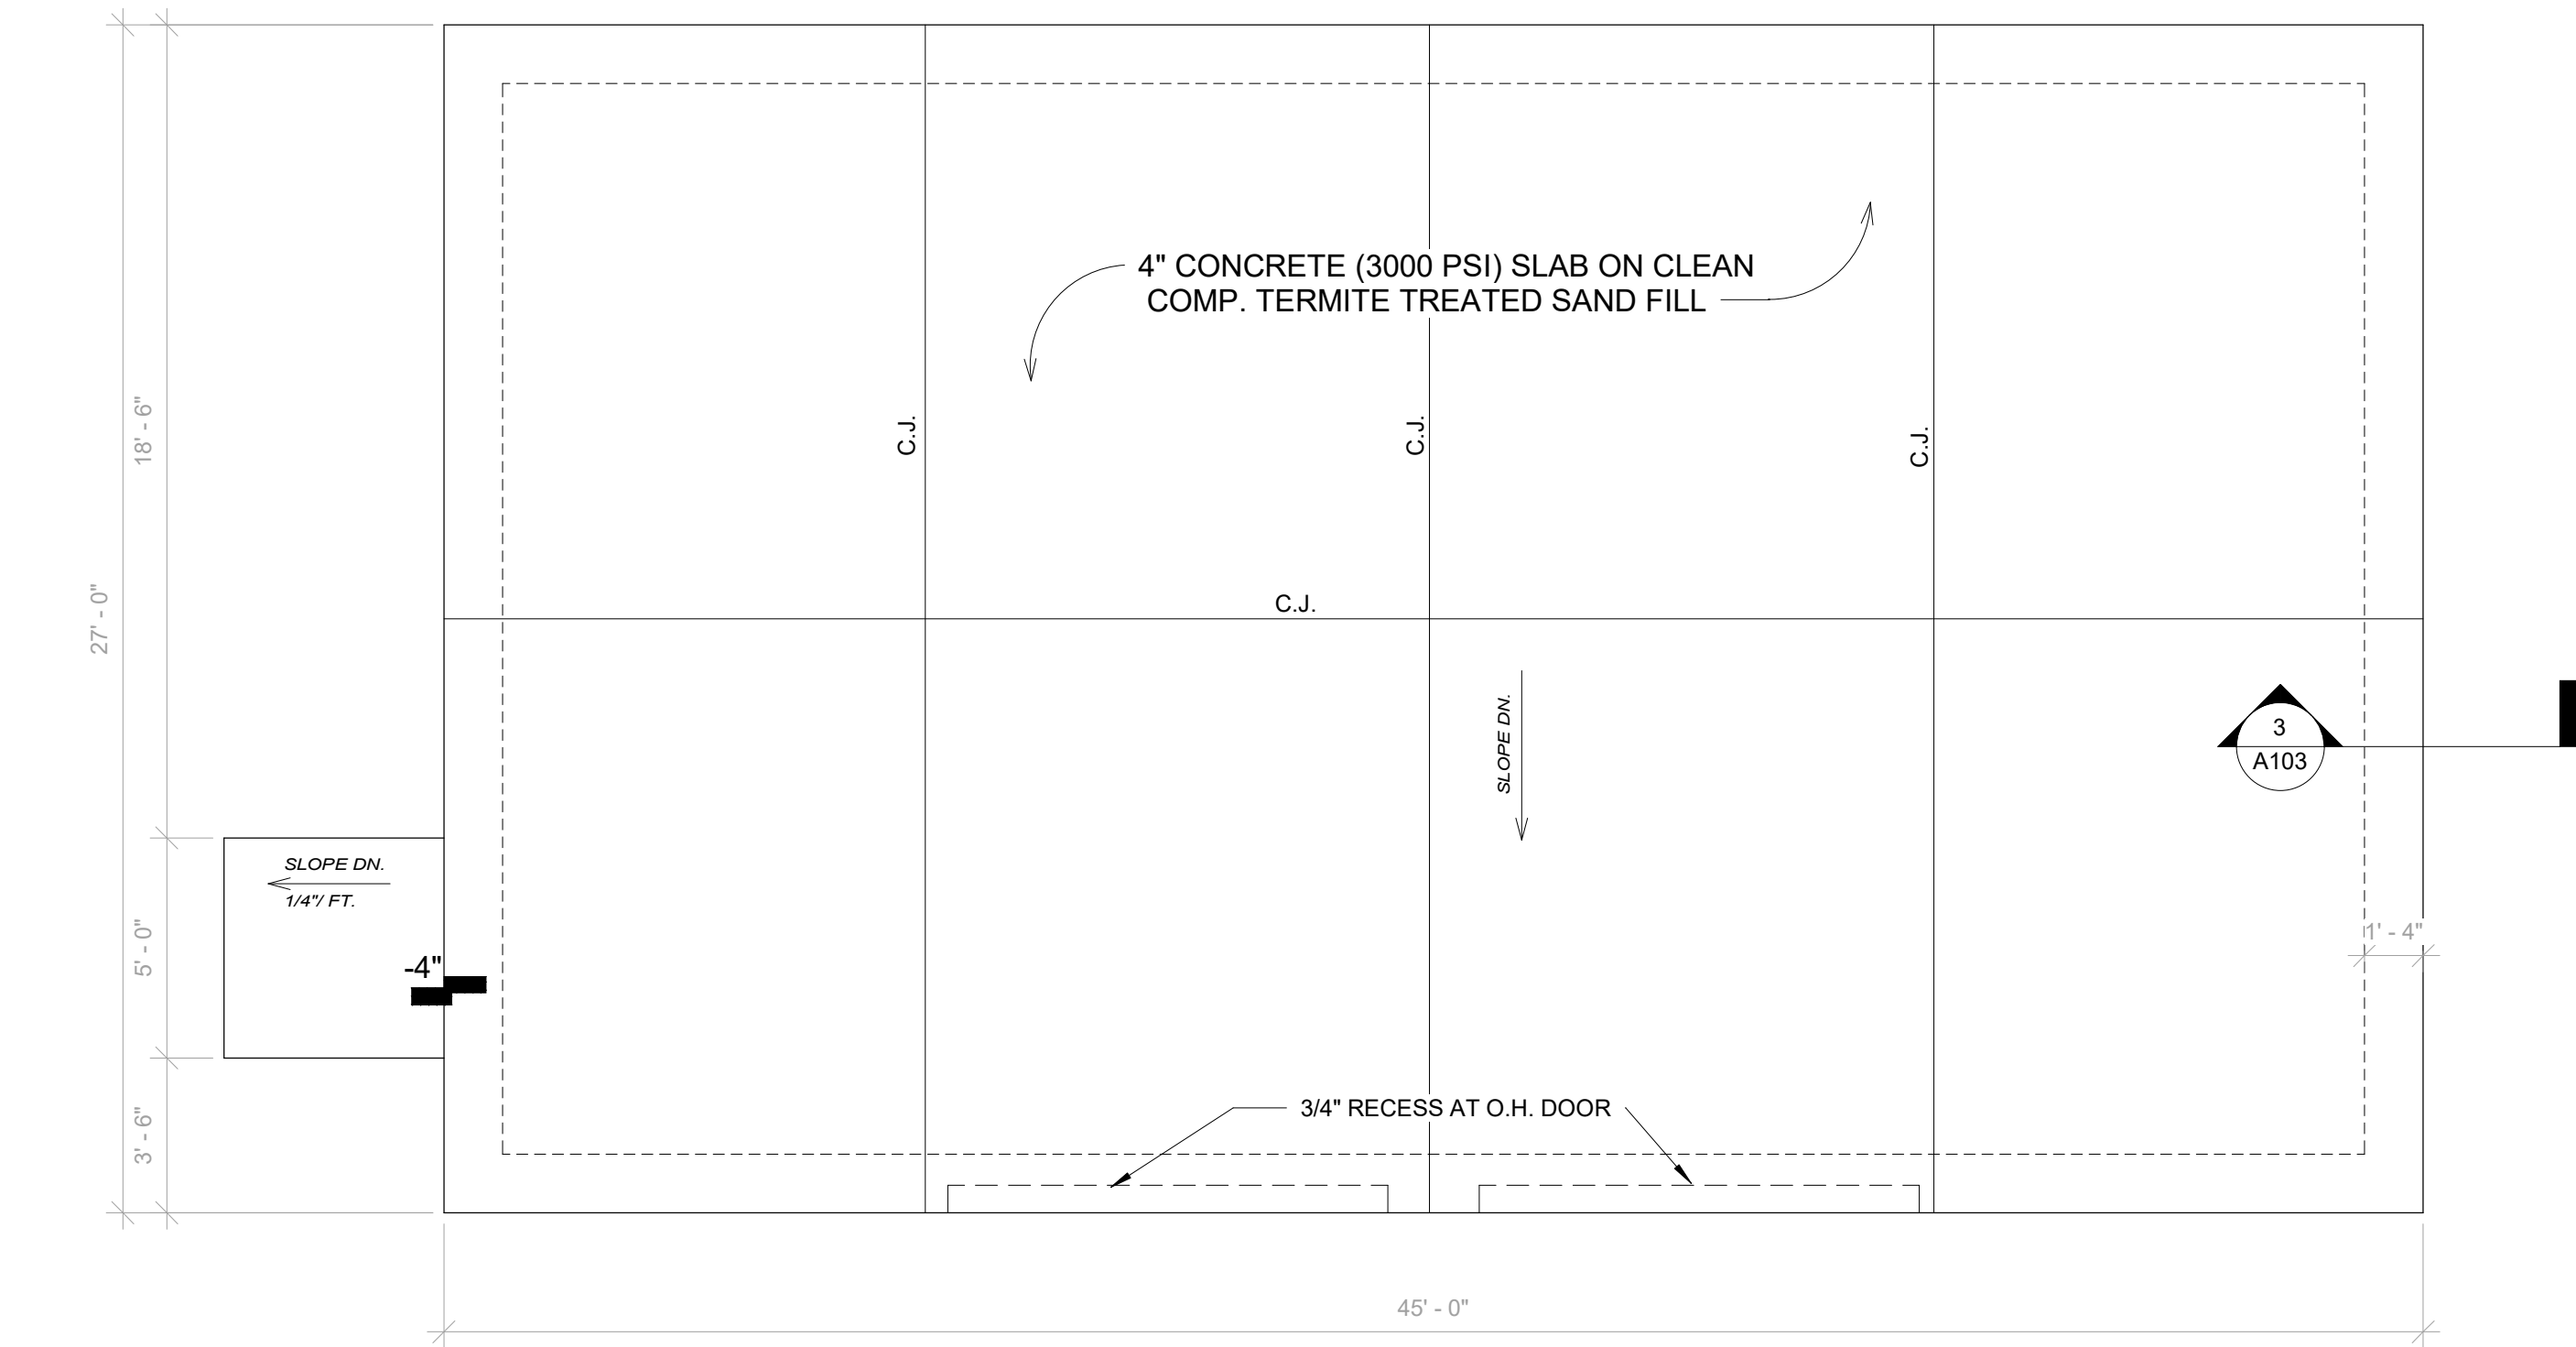

1 FOUNDATION PLAN
1/4" = 1'-0"

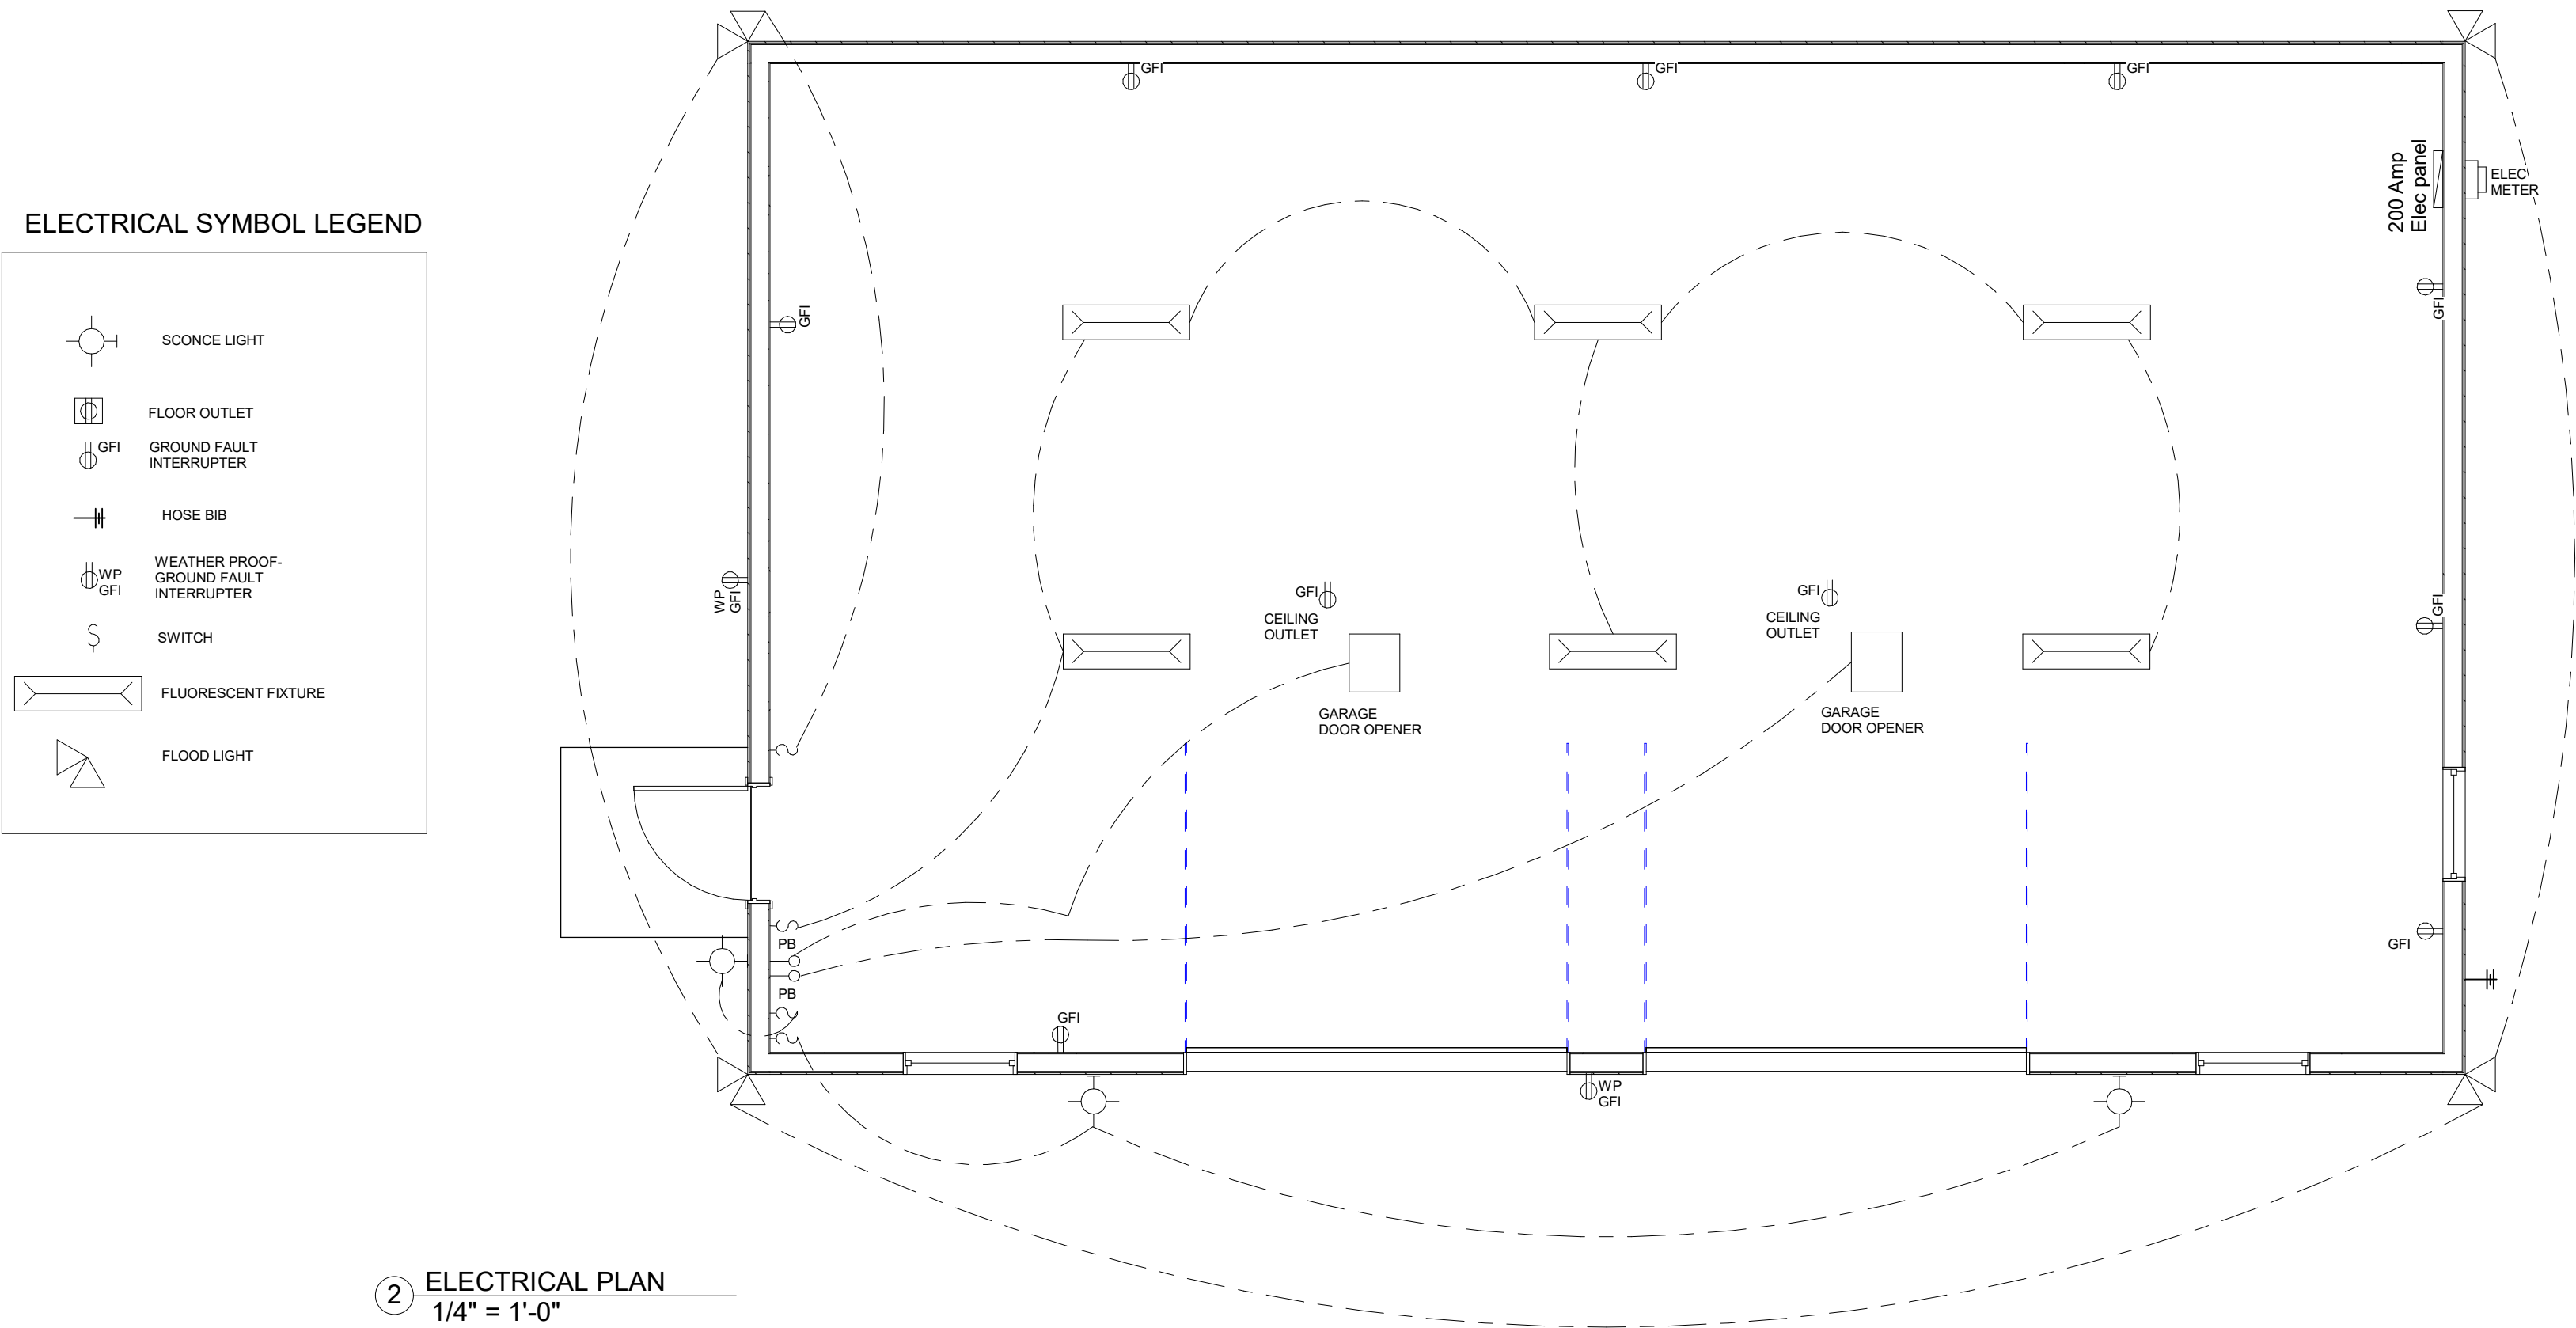

2 ELECTRICAL PLAN
1/4" = 1'-0"

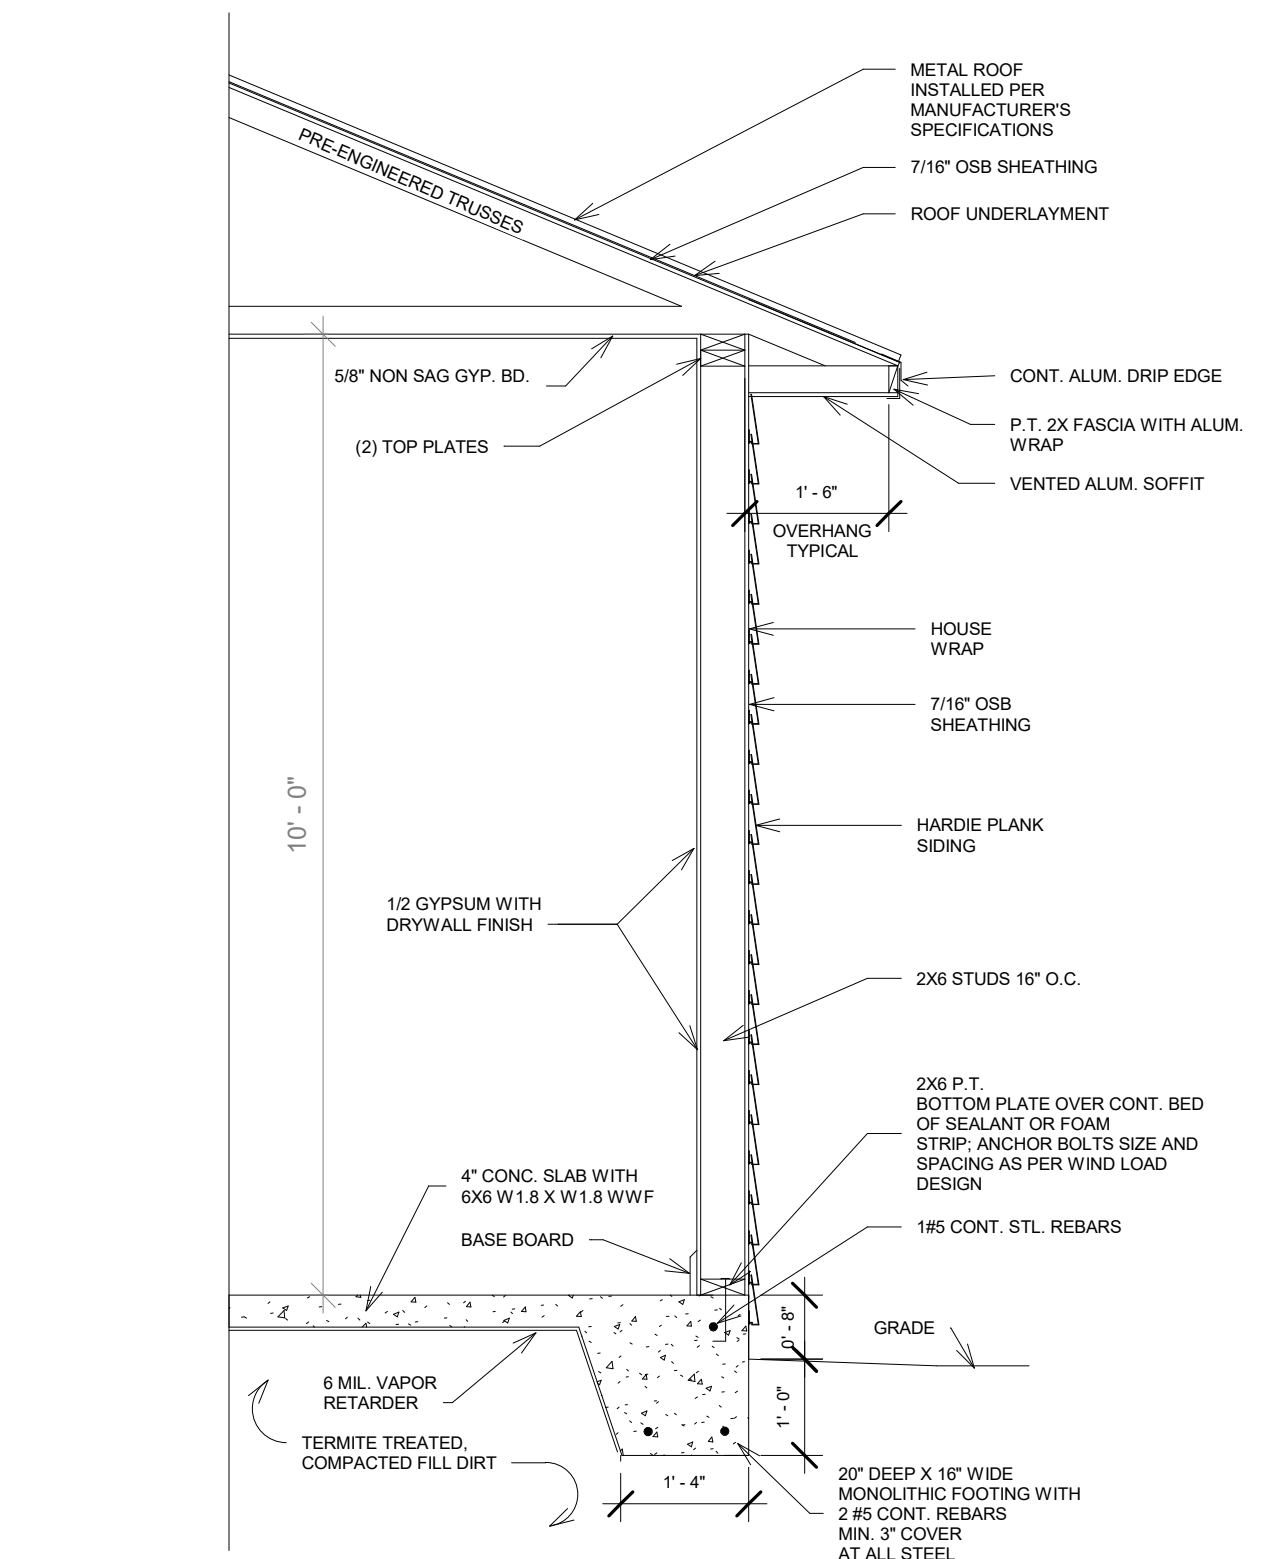

3 TYPICAL WALL SECTION
1/2" = 1'-0"

NEW COTTAGE FOR
BILL & SANDY TODD
FOUNDATION PLAN/
ELECTRICAL PLAN

Project number
Date
Drawn by
Checked by

Project Number
6-24-2023
MM
NN

A103

Scale
As indicated