



NOT FOR
CONSTRUCTION
(STRUCTURE
ENGINEER NEED
TO SIZE,
CALCULATE AND
VERIFY ALL
STRUCTURAL
ELEMENTS)

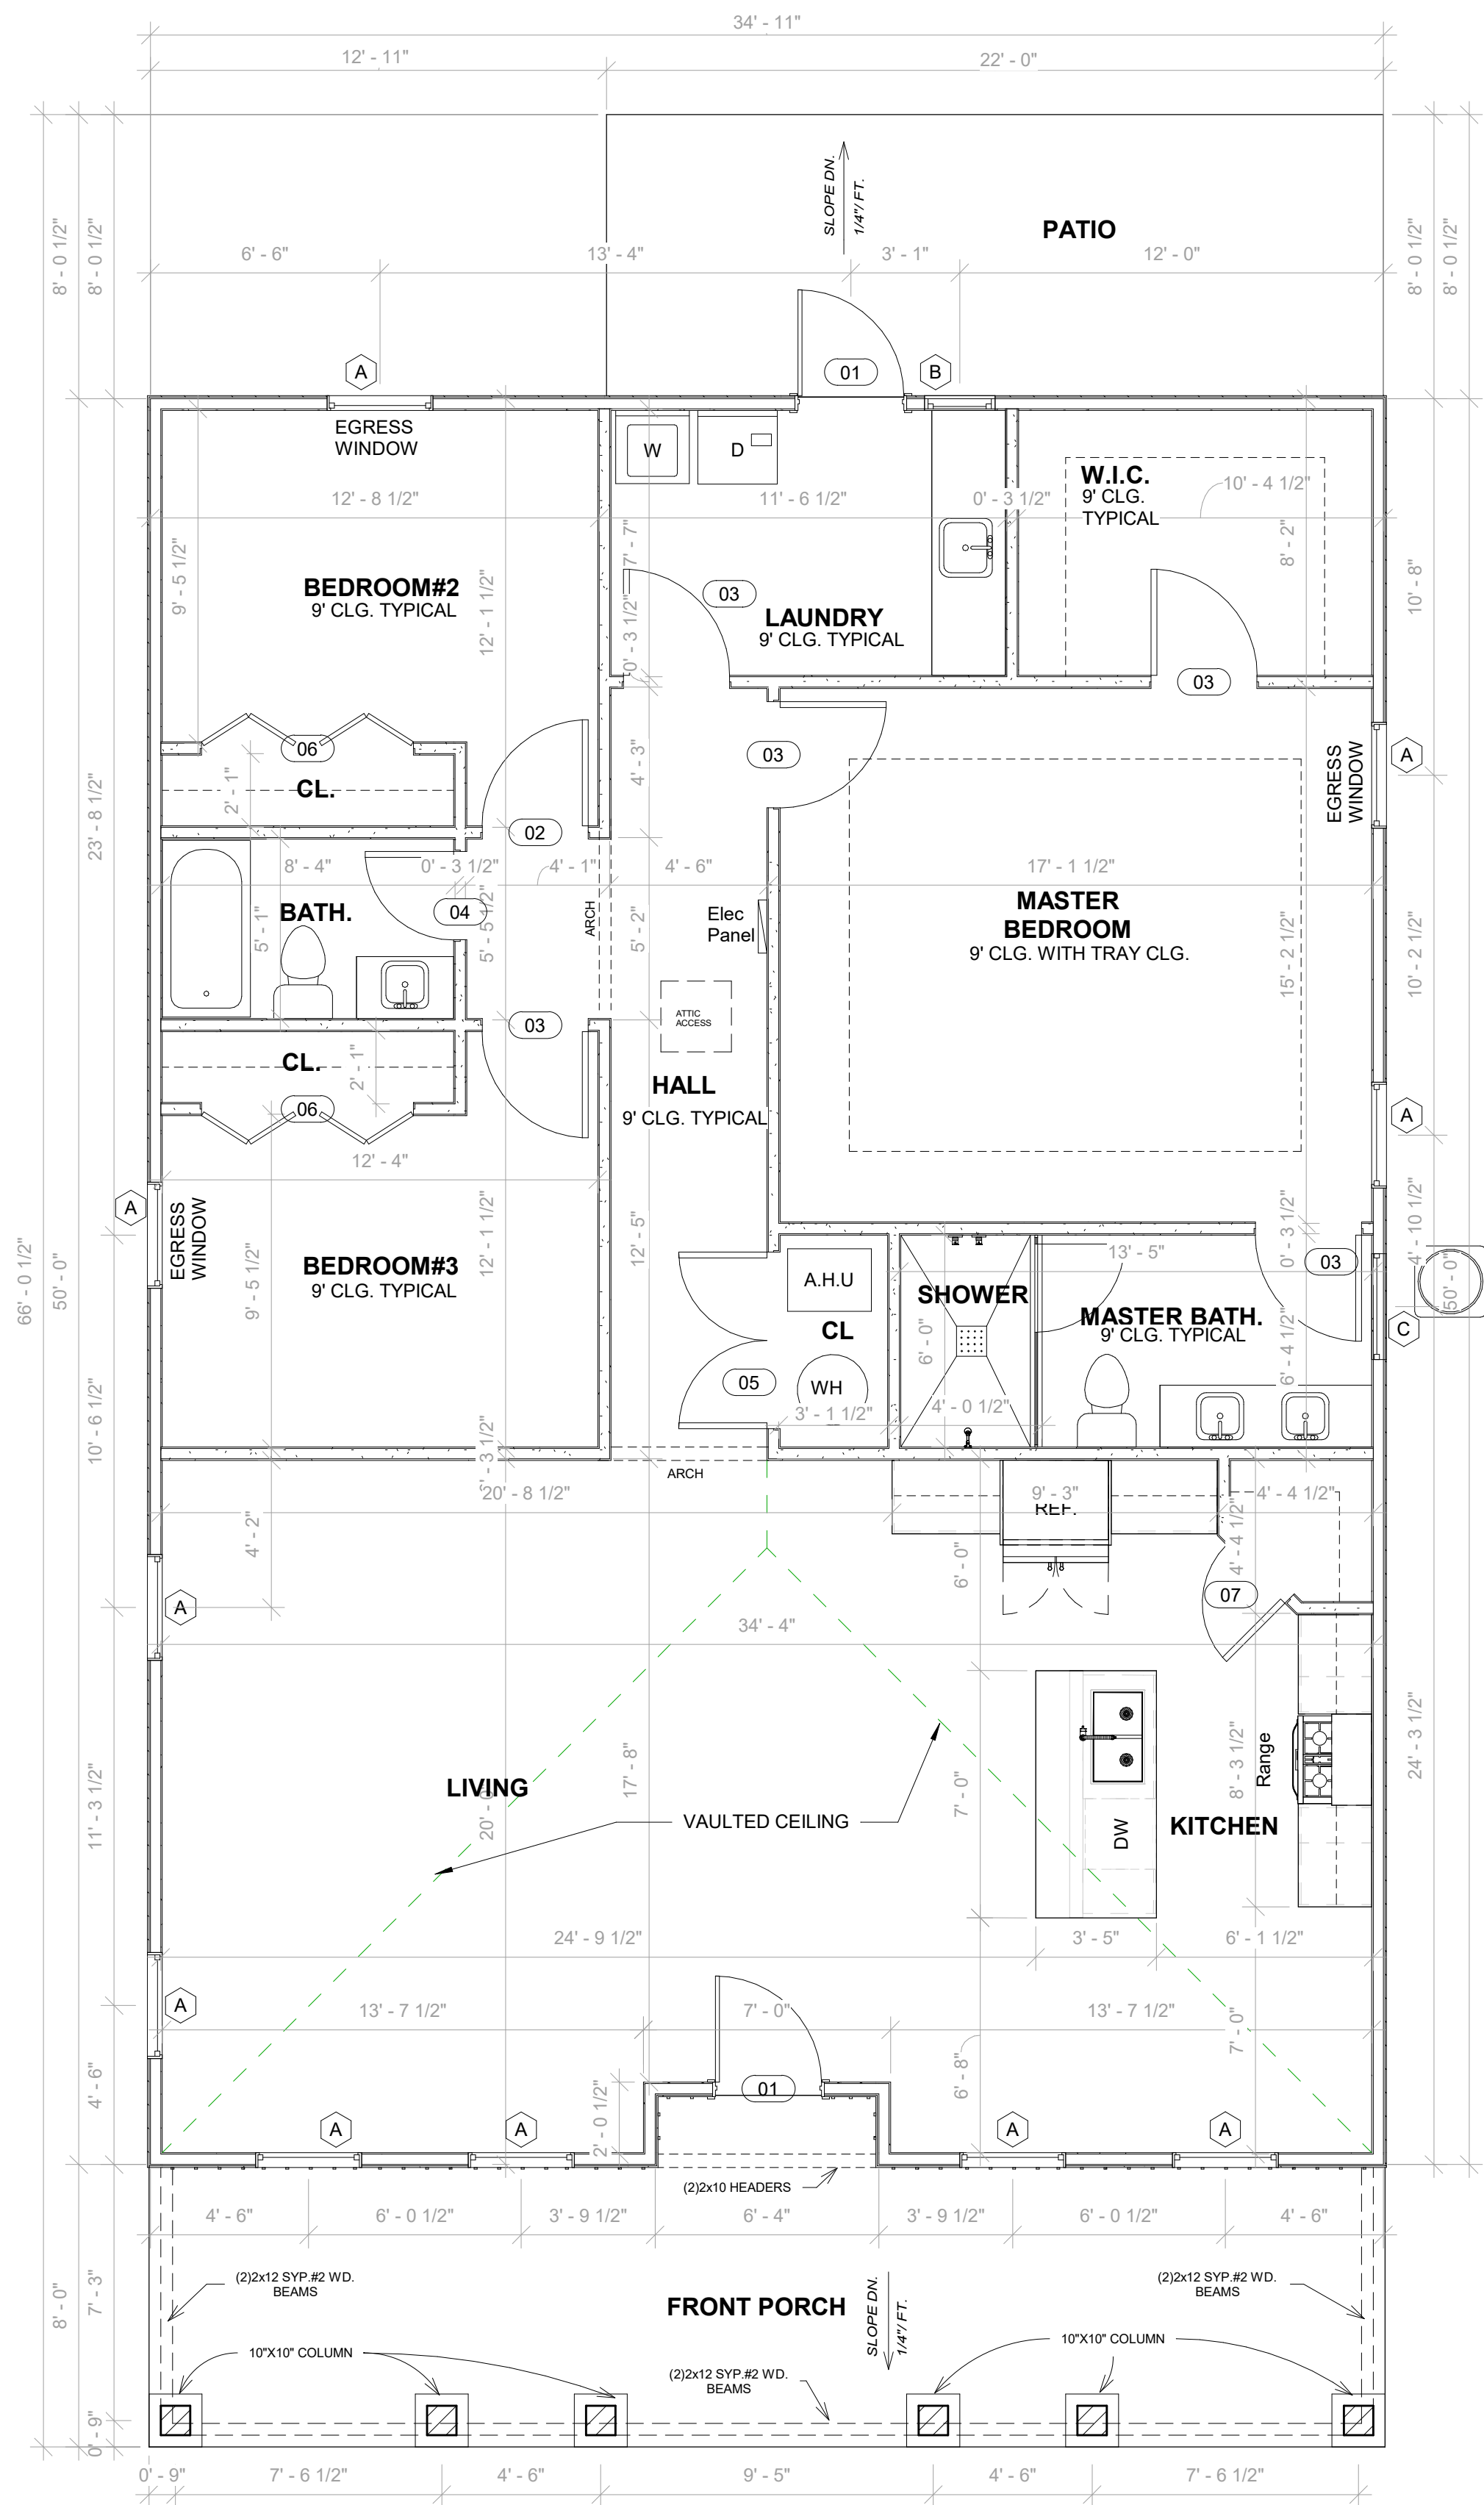

1 FLOOR PLAN
1/4" = 1'-0"

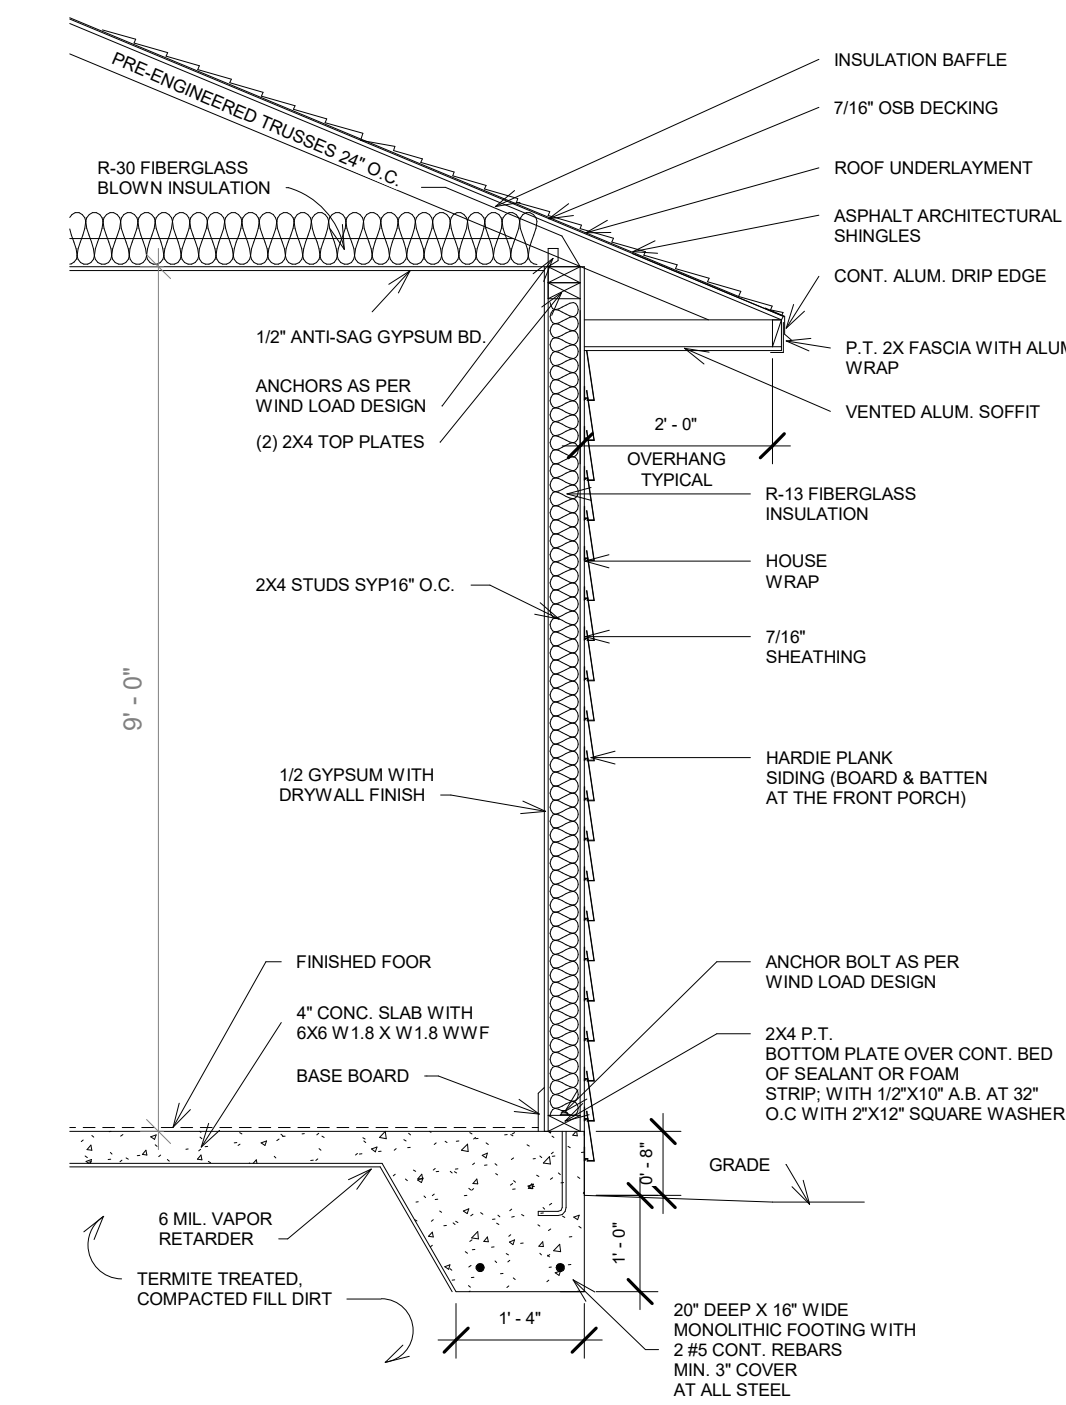

2 TYPICAL WALL SECTION
1/2" = 1'-0"

Door Schedule				
Mark	Count	Width	Height	Comments

01	2	3' - 0"	6' - 8"	EXTERIOR DOOR
02	1	3' - 0"	6' - 8"	INTERIOR DOOR
03	5	3' - 0"	6' - 8"	INTERIOR DOOR
04	1	2' - 6"	6' - 8"	INTERIOR DOOR
05	1	5' - 0"	6' - 8"	INTERIOR DOOR
06	2	6' - 0"	6' - 8"	INTERIOR DOOR
07	1	2' - 4"	6' - 8"	INTERIOR DOOR

Grand total: 13

Window Schedule				
Mark	Count	Type	Head Height	Comments

A	10	3-0 5-0 SH	6' - 8"	
B	1	2-0 3-0 SH	6' - 8"	
C	1	1-4 3-0 FIXED	6' - 8"	
D	2	1-4 2-0 FIXED	13' - 6"	DORMER WINDOW

Grand total: 14

NEW RESIDENCE
Suleyvi Villanueva

532 NW 29TH AVE GAINESVILLE, FL 32609

Date 1-28-2022

A101