


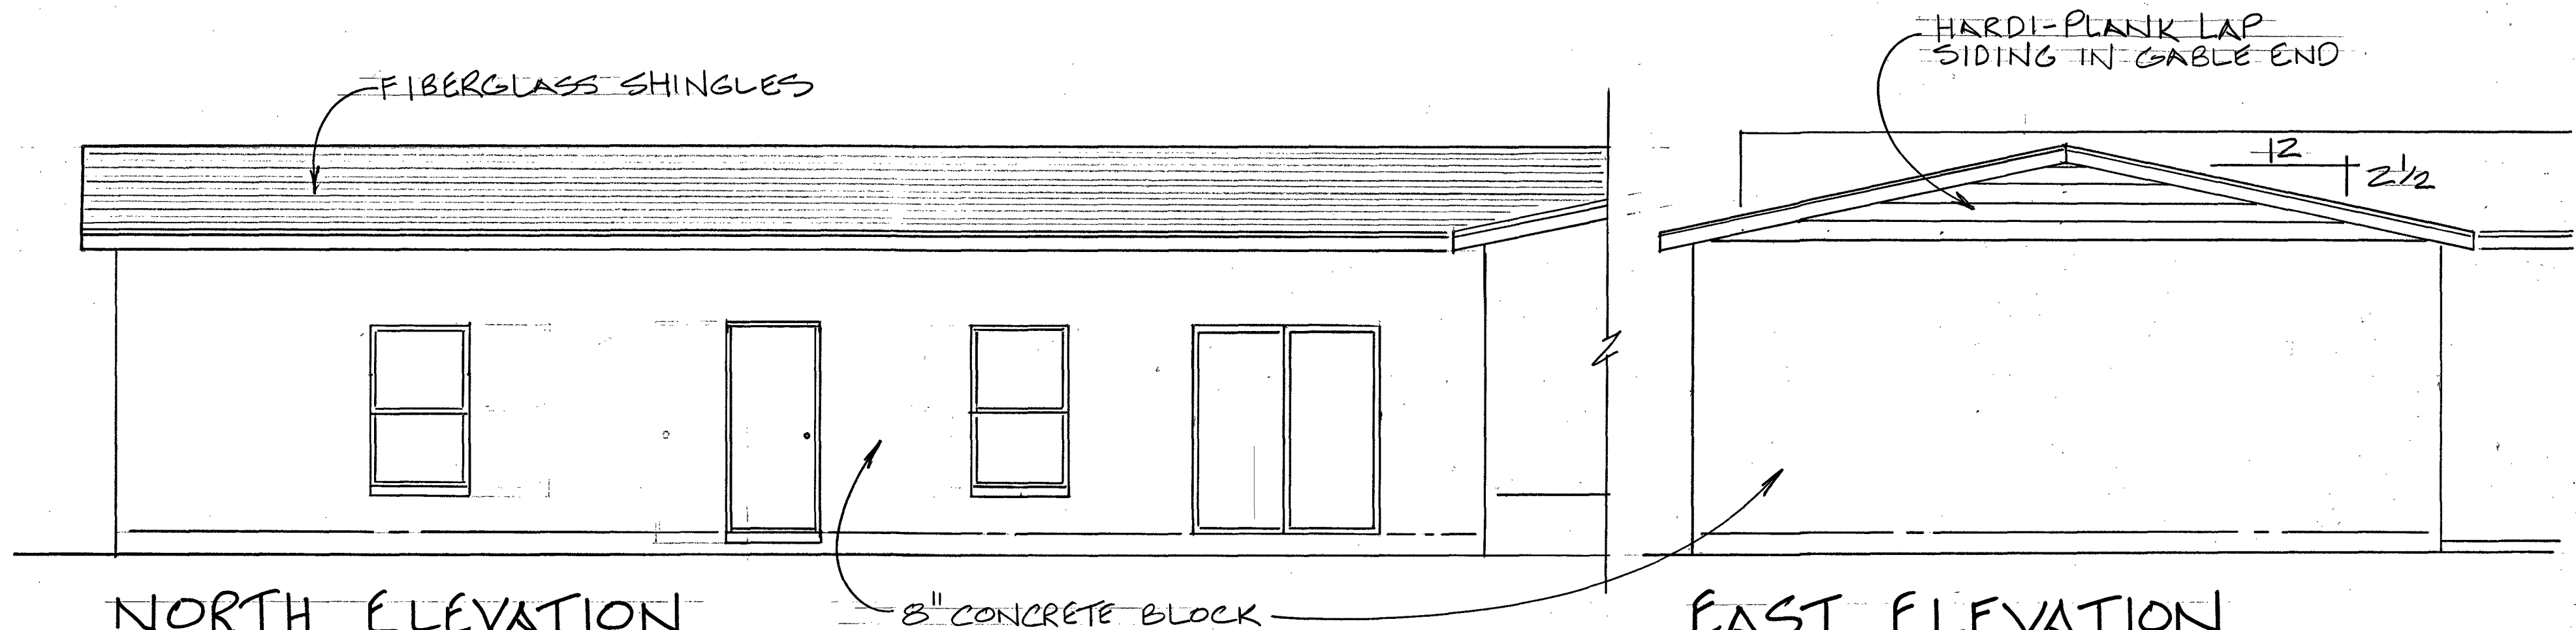

NORTH ELEVATION


$\frac{1}{4}'' = 1'-0''$

EAST ELEVATION

$\frac{1}{4}'' = 1'-0''$


NOTES:

1. ALL HORIZONTAL REBARS SHALL TIE AT ALL CORNERS A MIN. OF 24"
2. DROP CMU AS REQUIRED AT ALL DOORS AND EXPOSED PORCH SLAB EDGES.

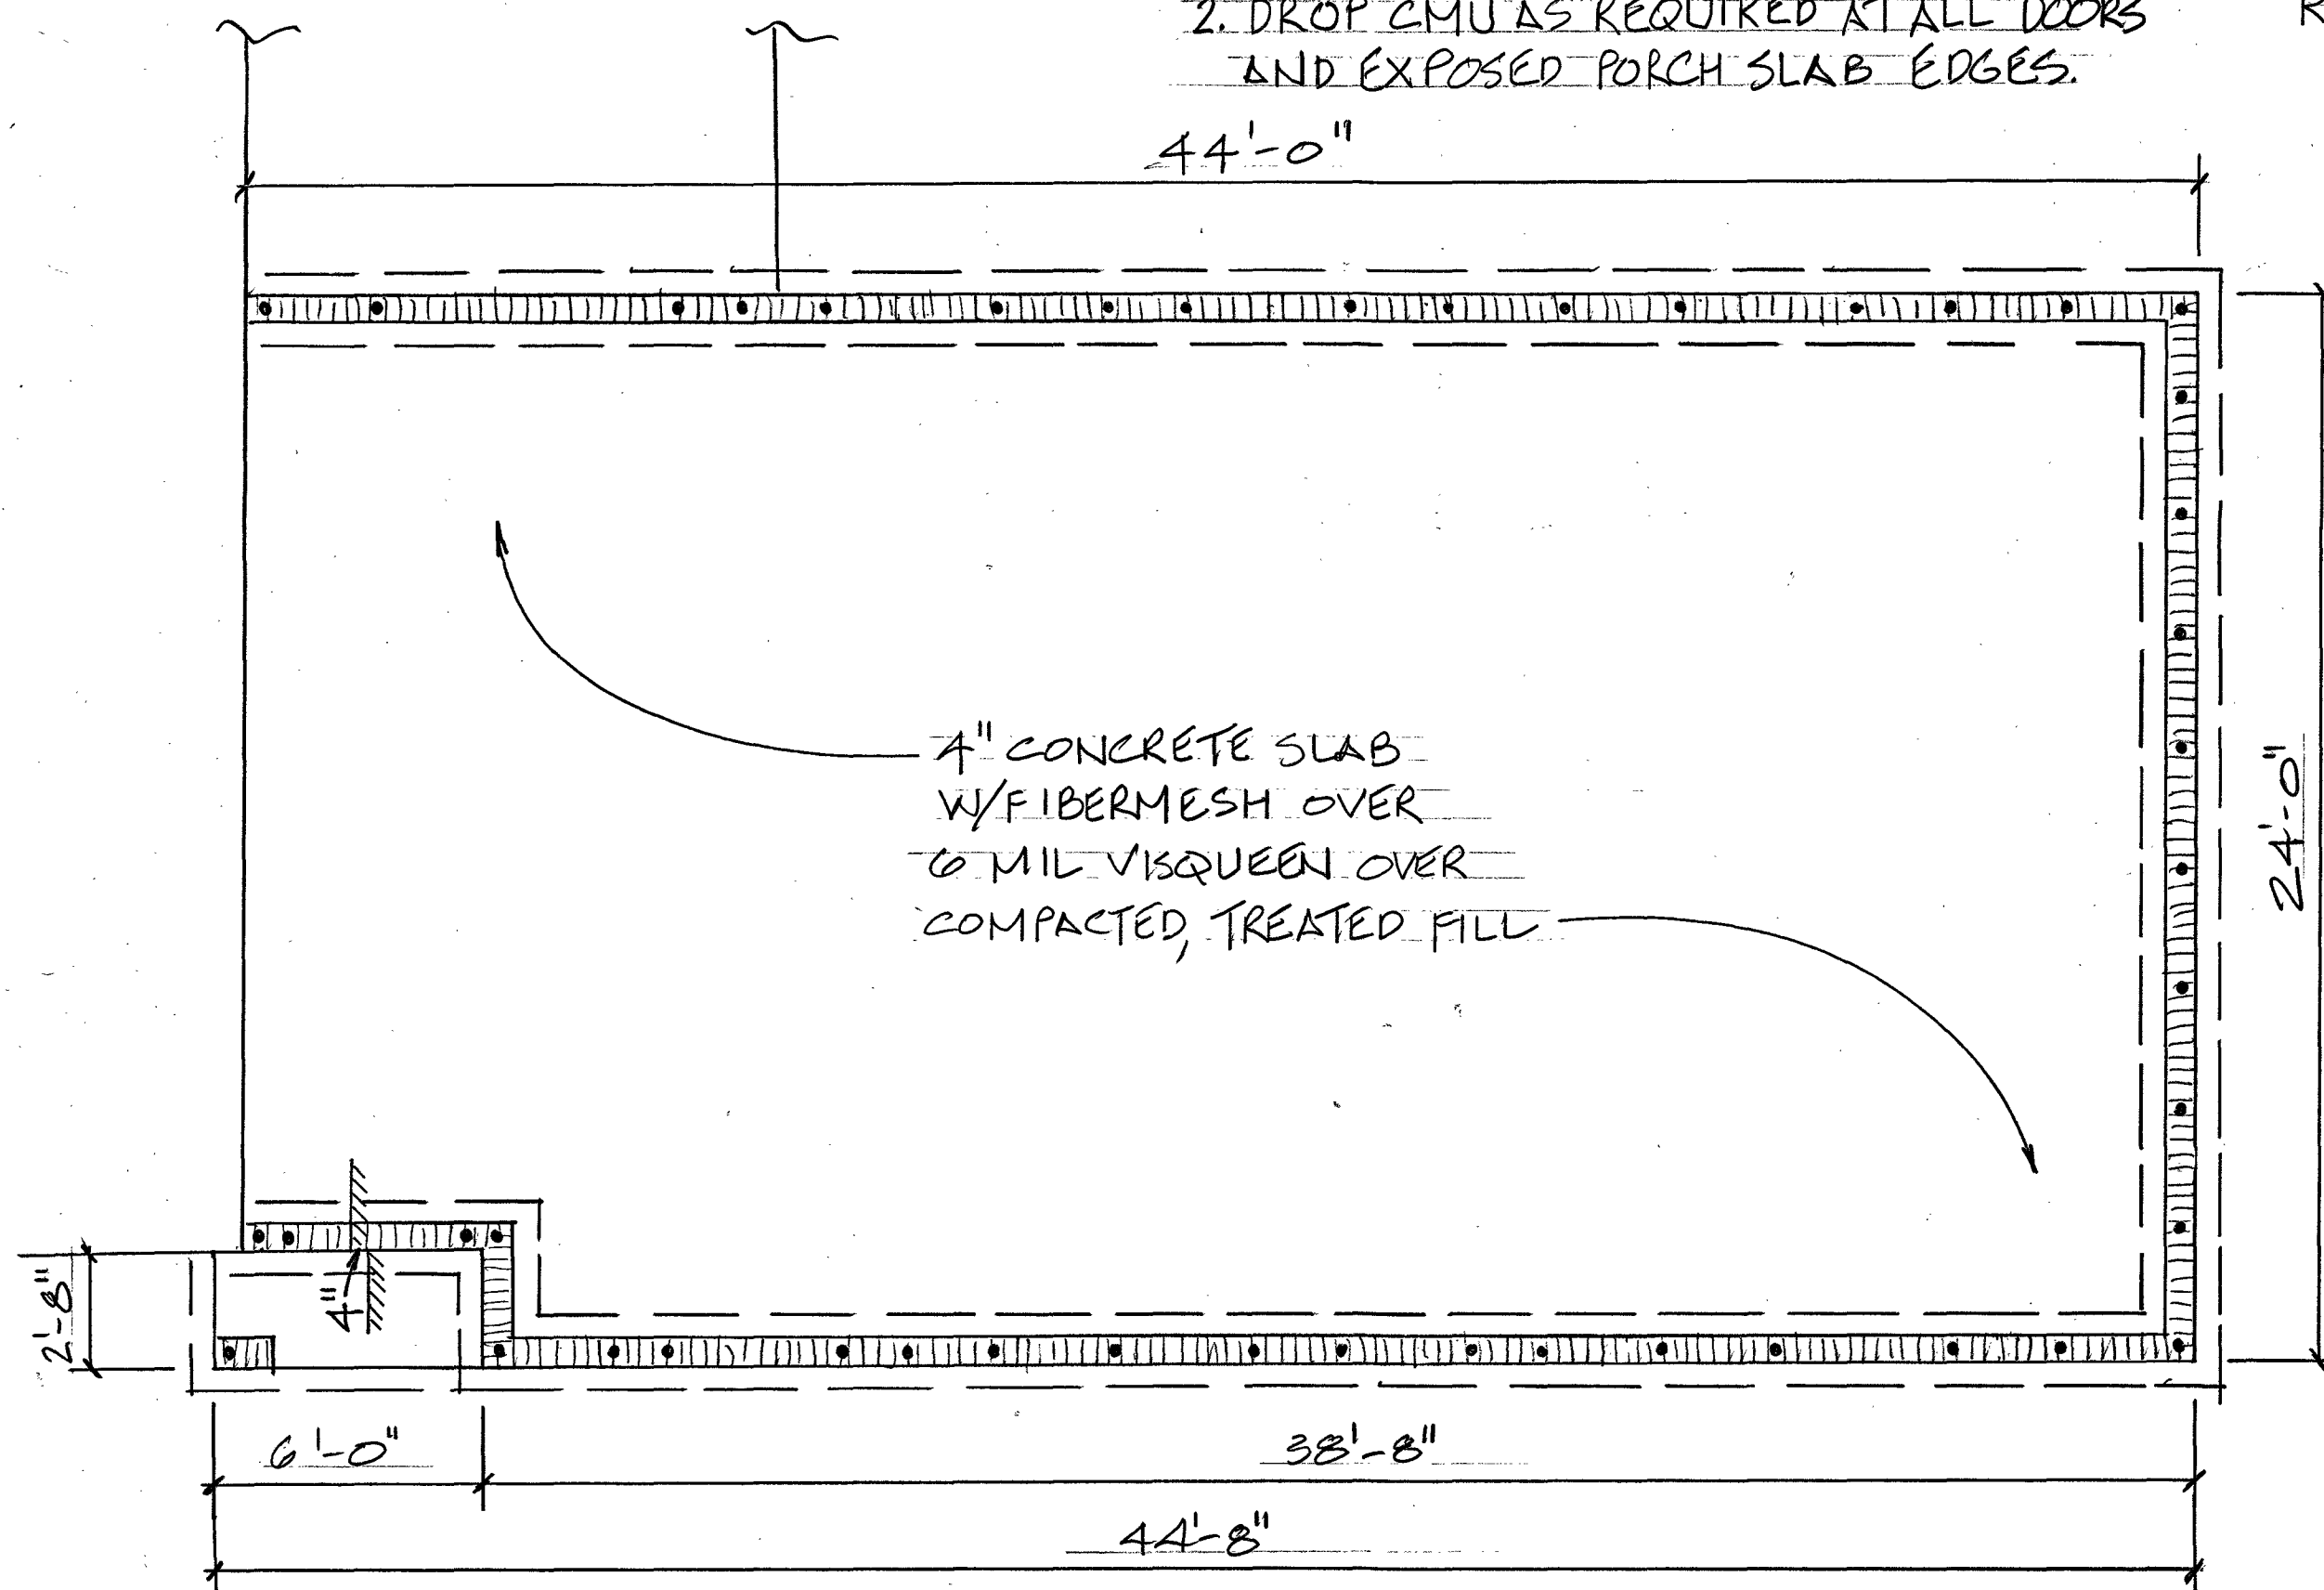

FOUNDATION PLAN

$\frac{1}{4}'' = 1'-0''$

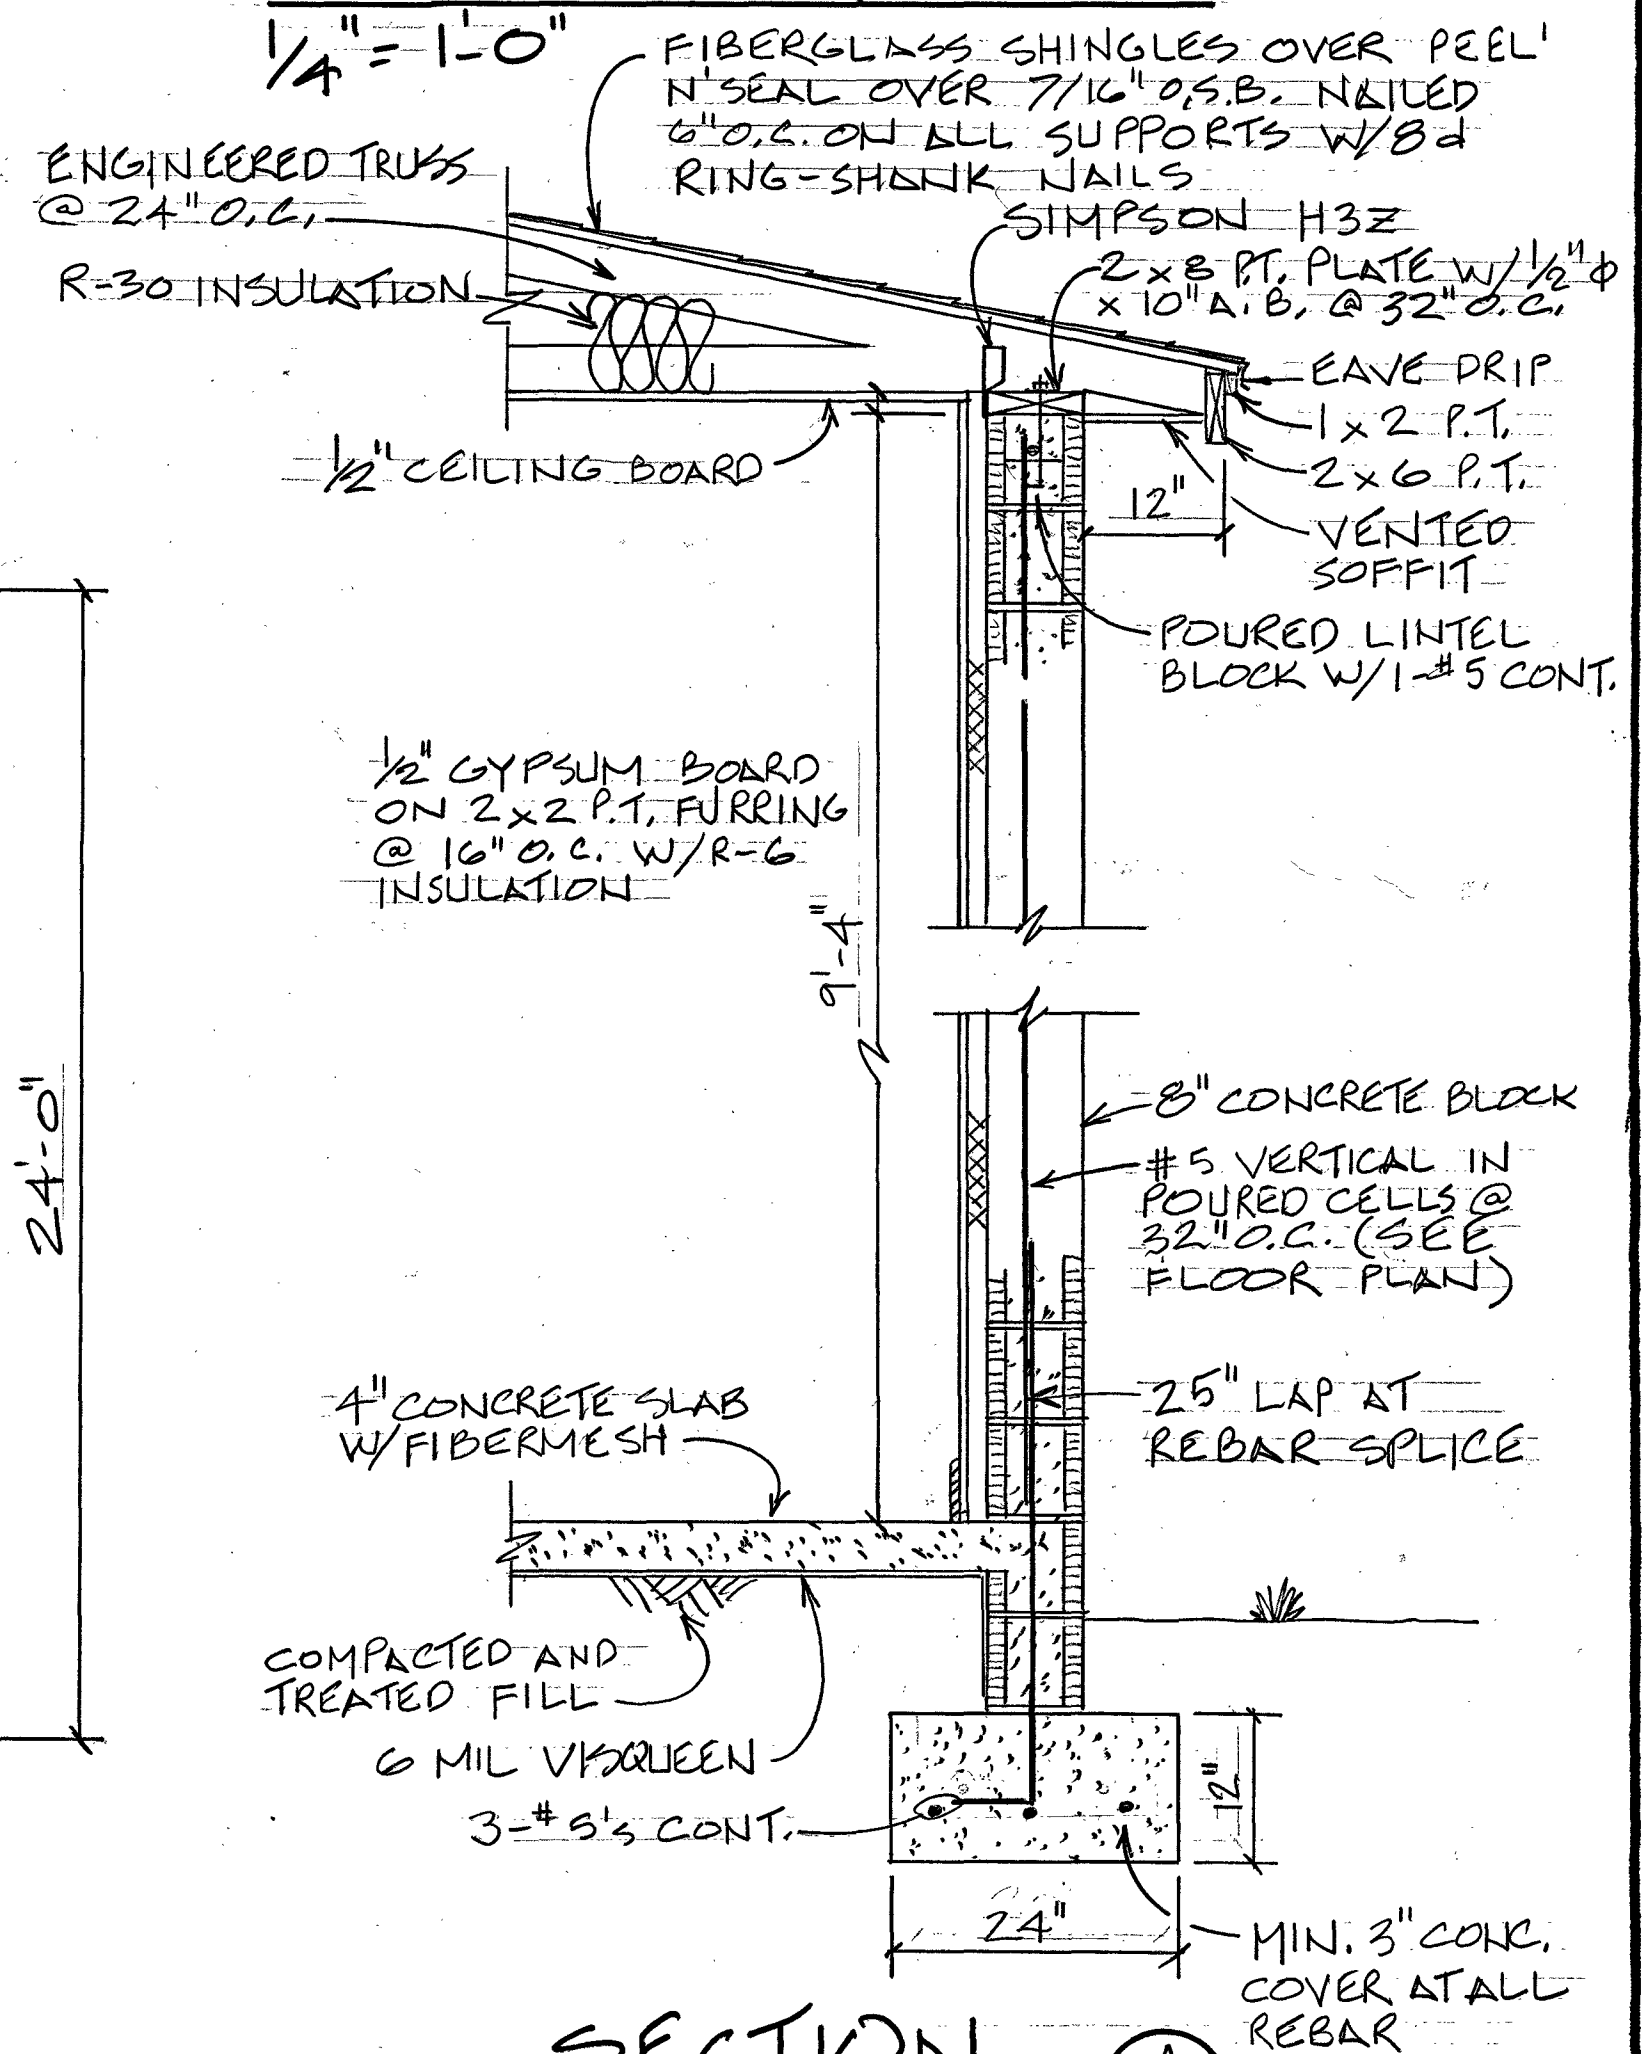

SECTION

$\frac{3}{4}'' = 1'-0''$

A
3

ADDITION TO RESIDENCE FOR:

MR. JEAN DOREUS

2709 CHARBRAY DR., JAX, FL. 32211

Date 5-16-23

Scale AS NOTED

Drawn CLG

Job

Sheet 3

Of 4 Sheets