




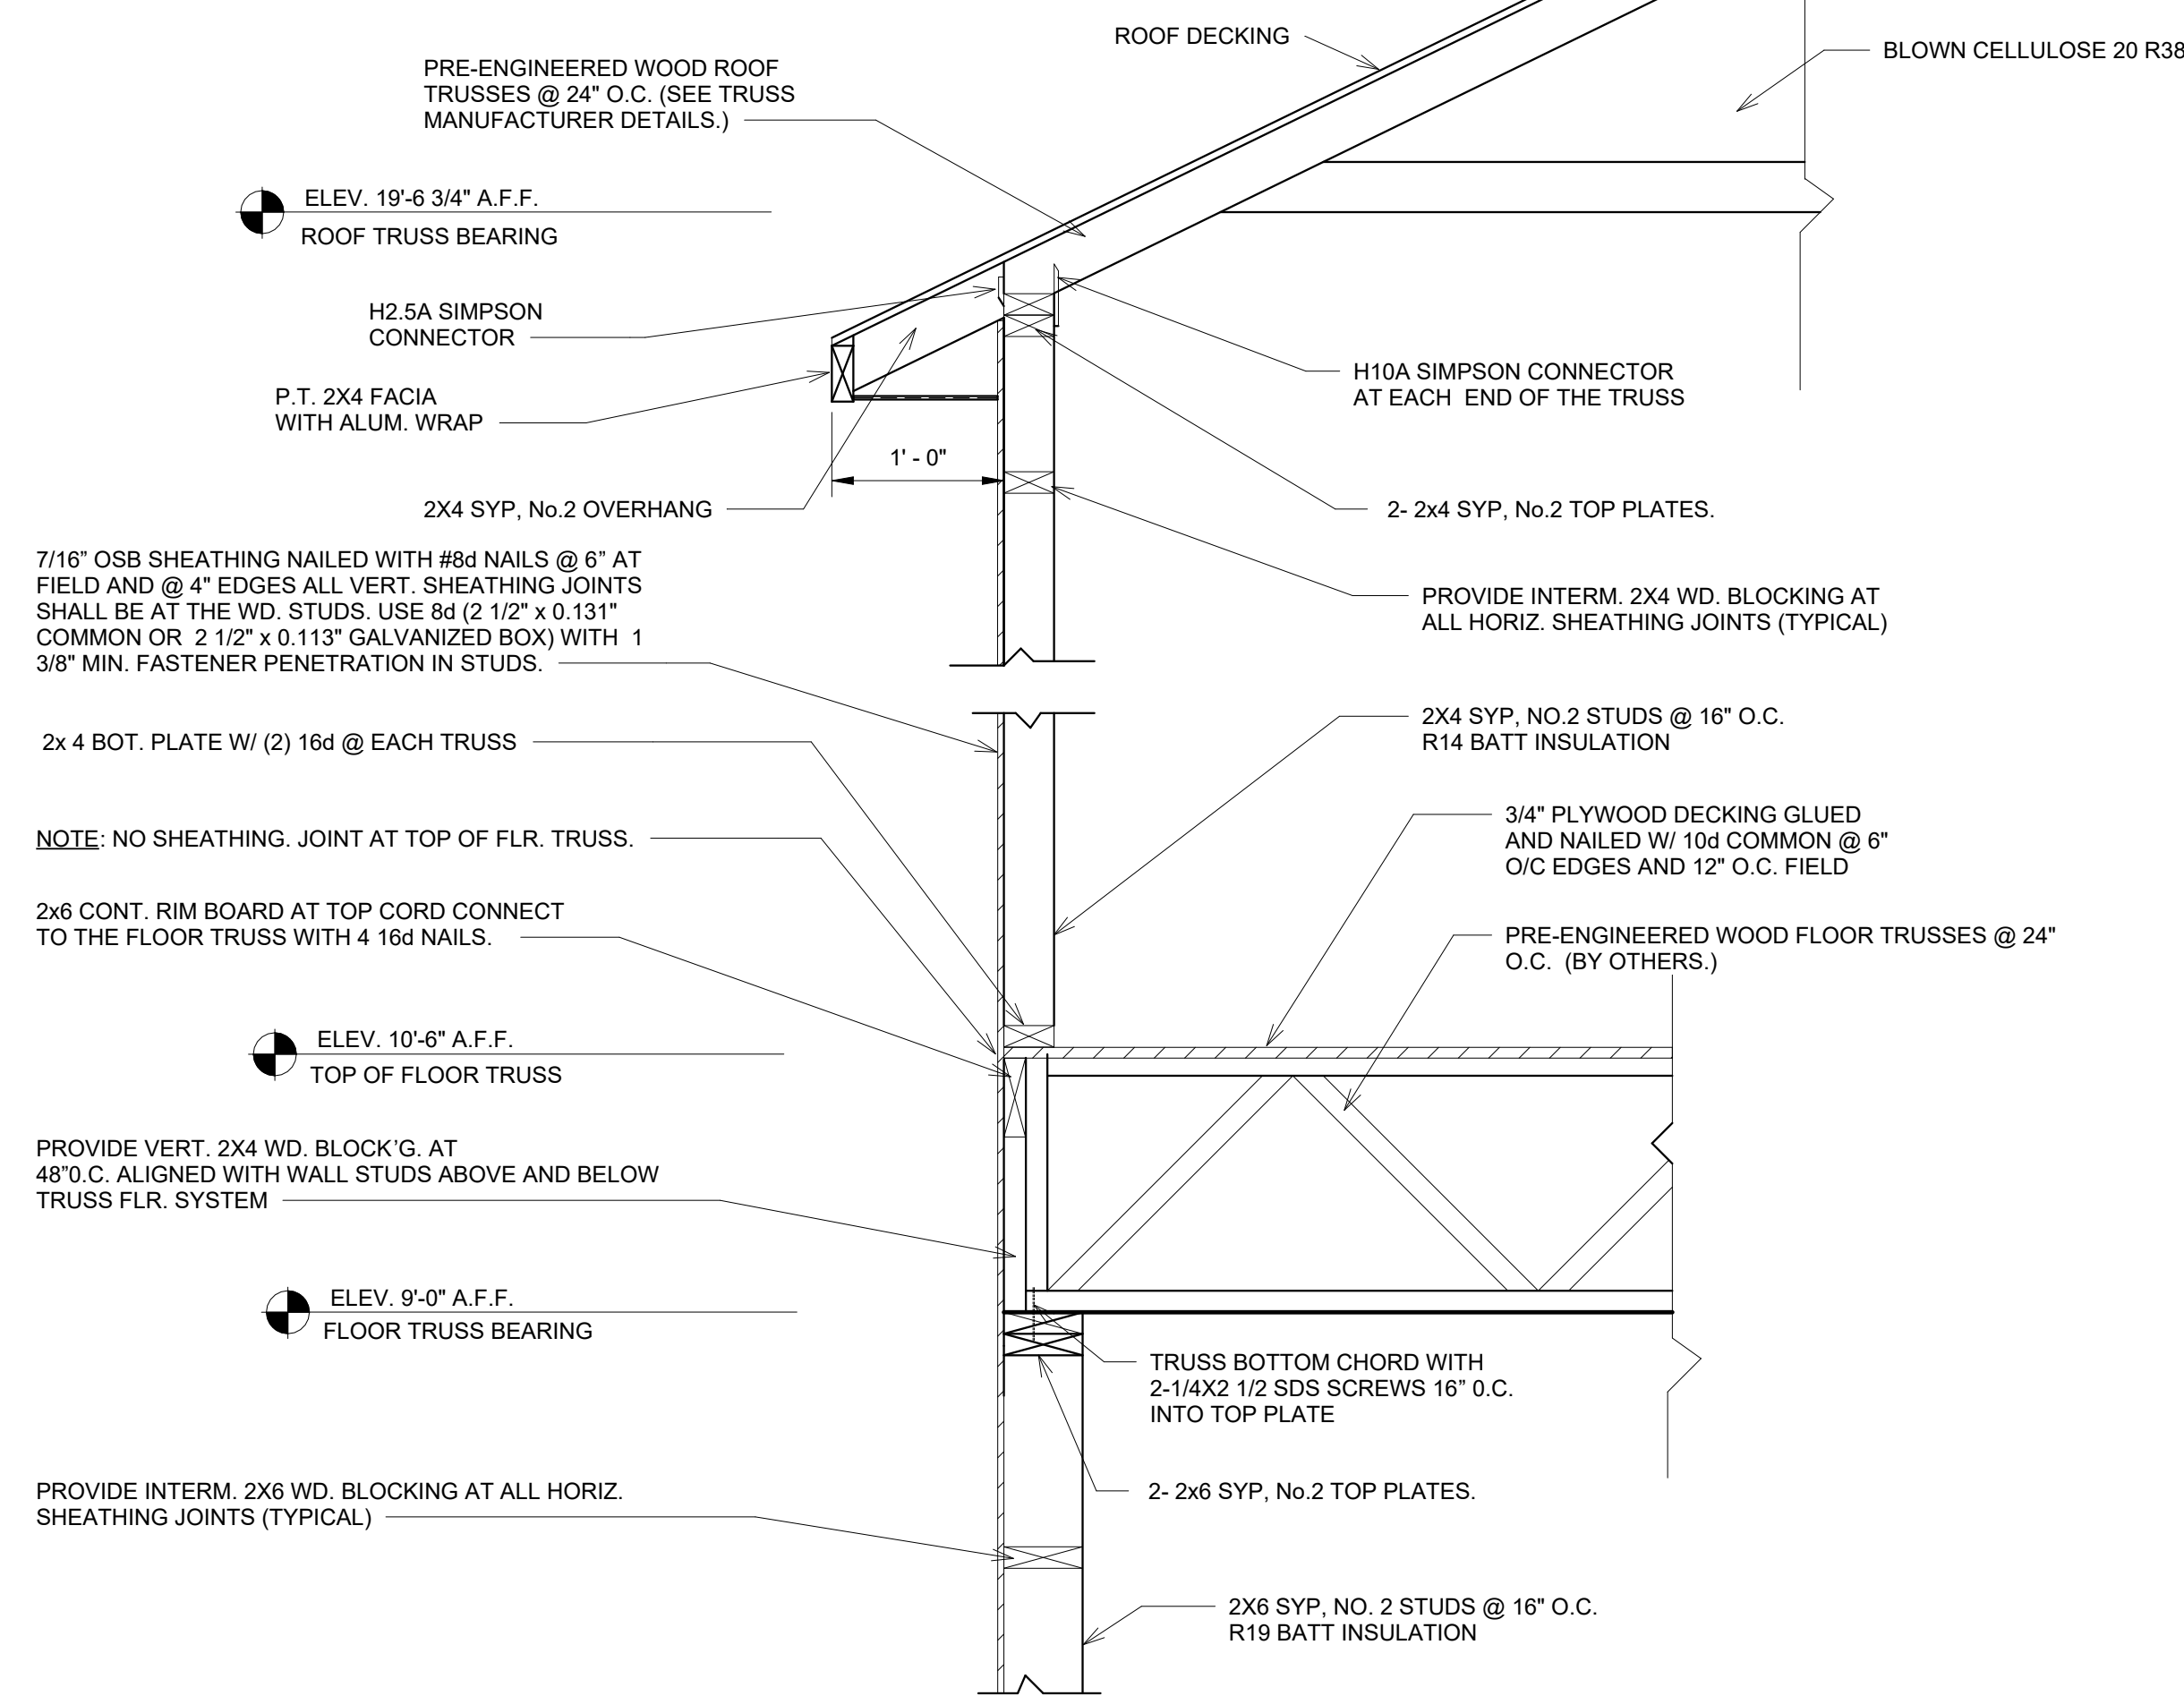

5 EXTERIOR WALL SECTION_2
1" = 1'-0"

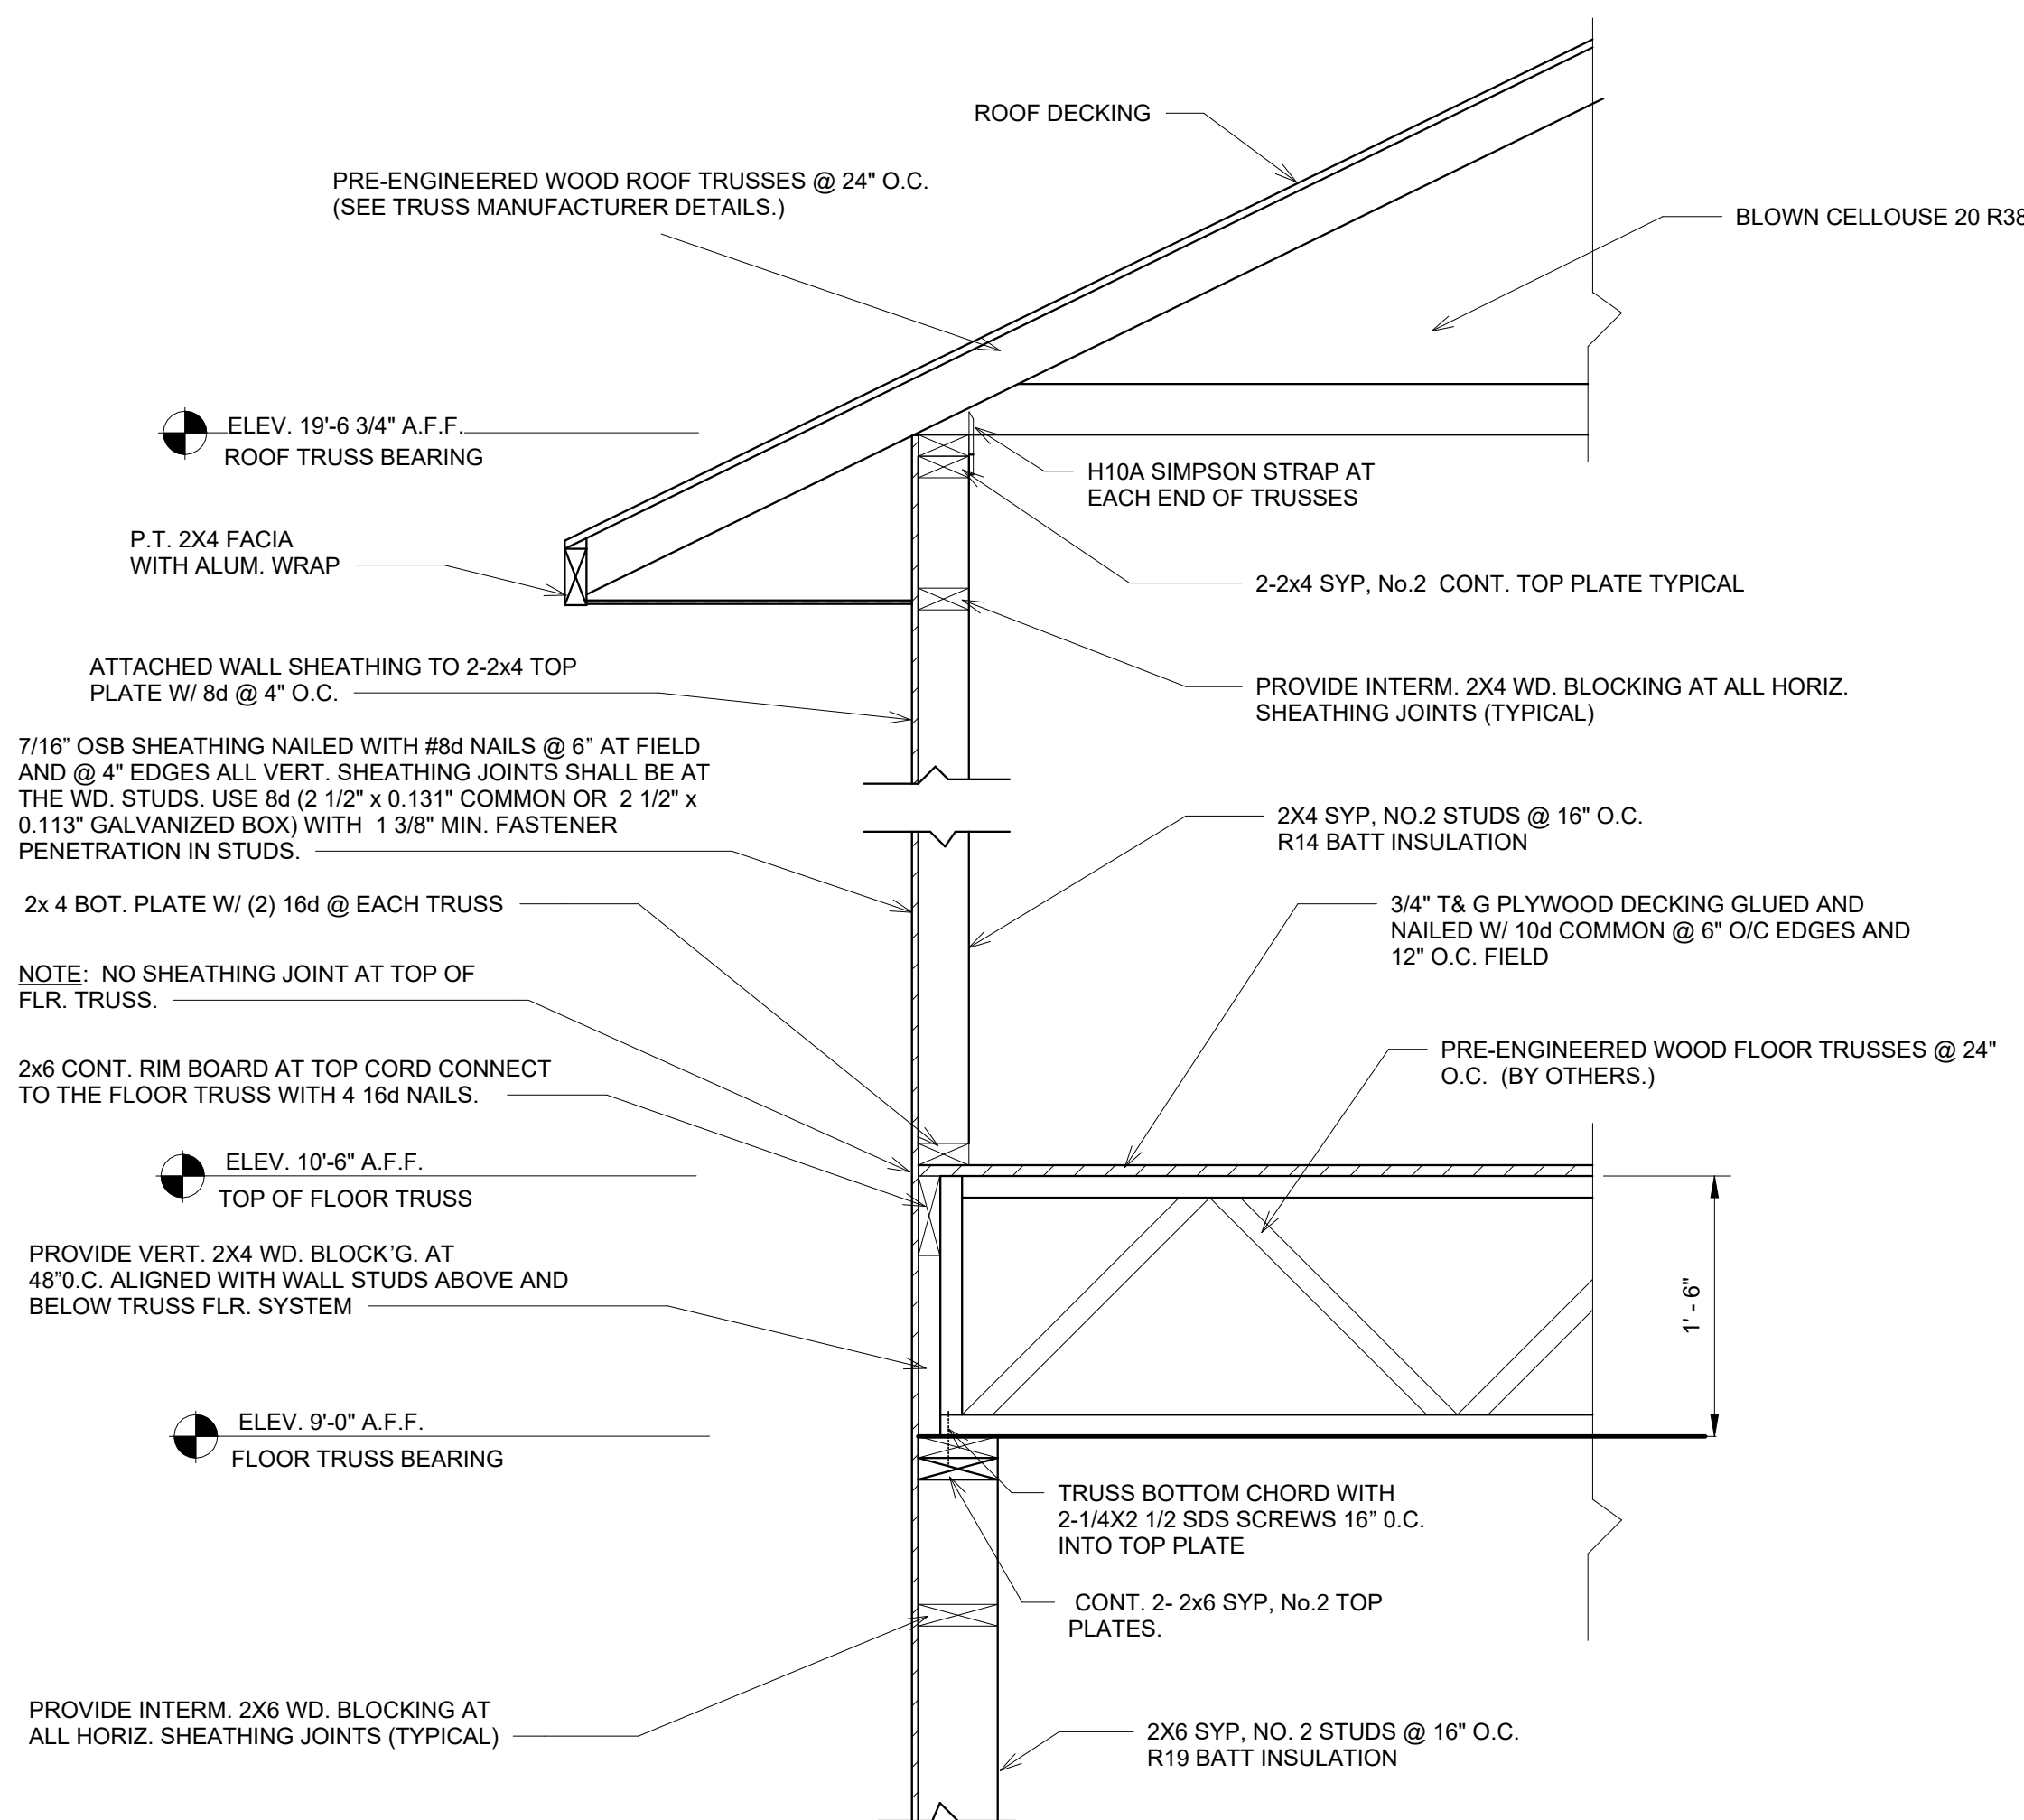

6 EXTERIOR WALL SECTION_1
1" = 1'-0"

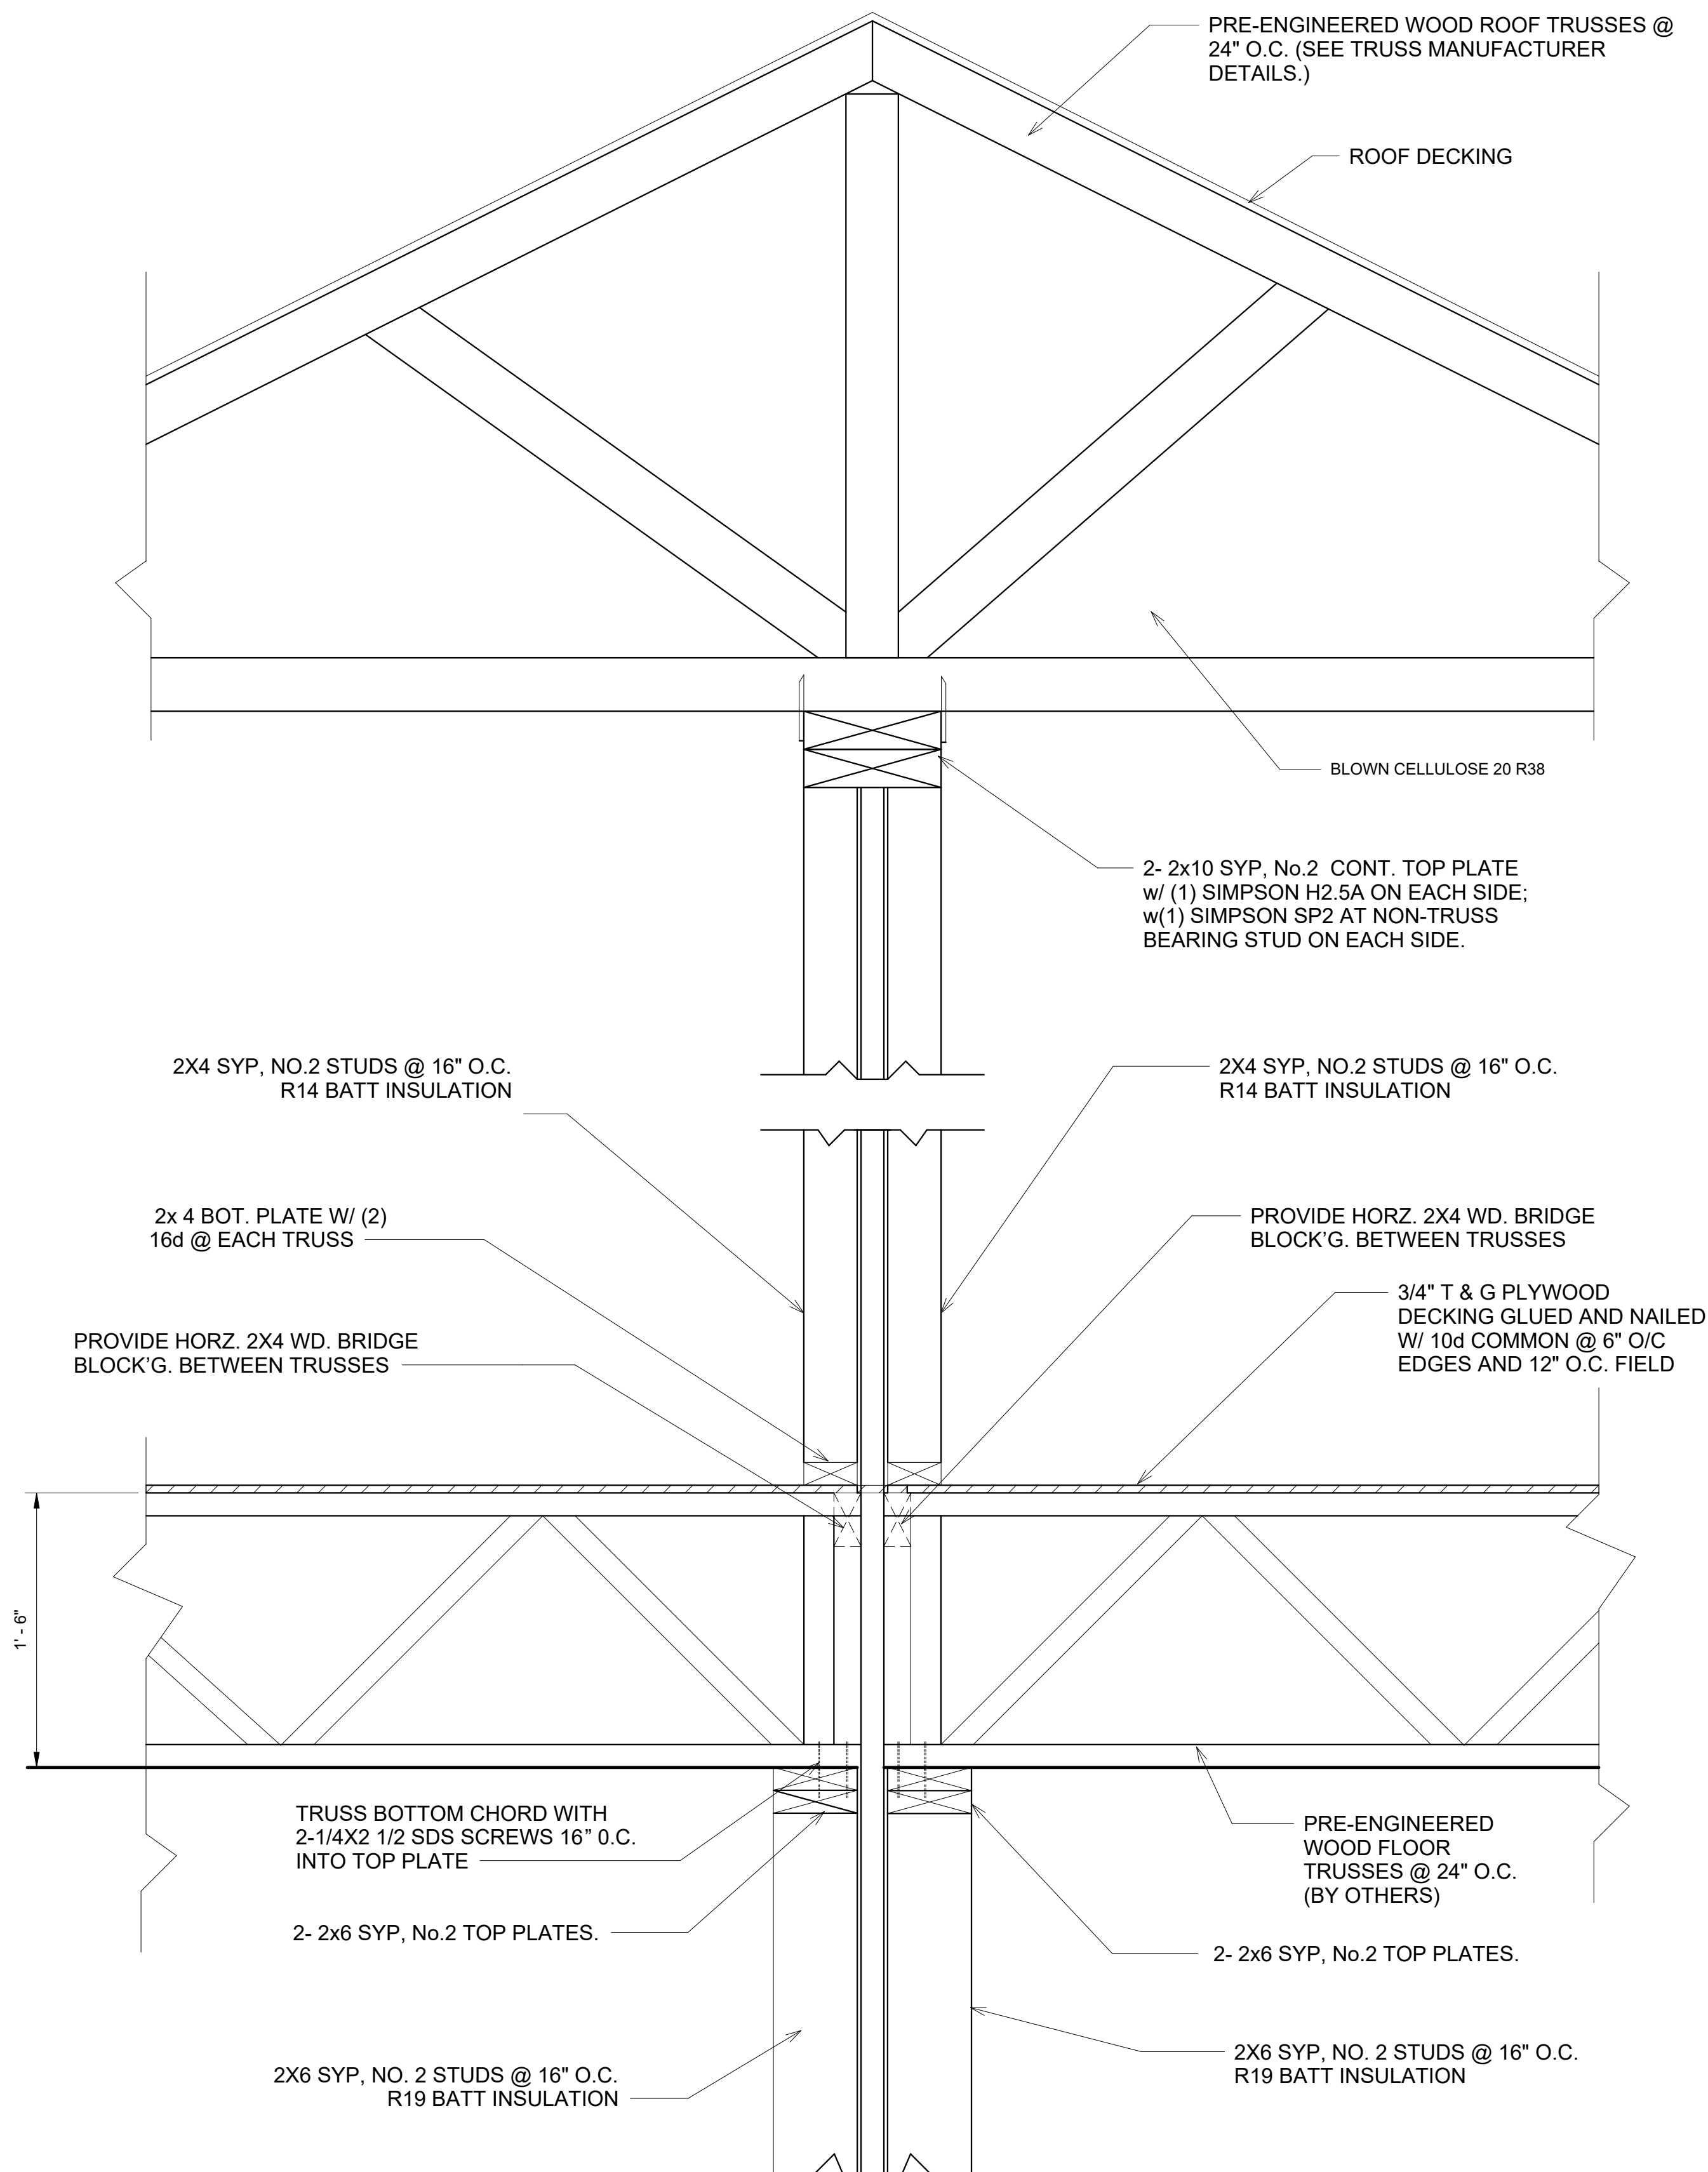

1 INTERIOR WALL SECTION
1 1/2" = 1'-0"

TECH 101 LLC

N. Nawari, P.E.

Address:
1210 NW 106th ST.
Gainesville, FL 32060
Phone: 330-573-6640
e-mail: Nnawari1@gmail.com

Project:
Sergio Lanata
LANATA COTTAGE
NEIGHBORHOOD,
ALACHUA COUNTY,
FLORIDA

[illegible]

Sergio Lanata

Lanata Cottage

Wall Sections

Project number	Project Number
Date	Issue Date
Drawn by	Author
Checked by	Checker

S 4.0

Scale	As indicated
-------	--------------