



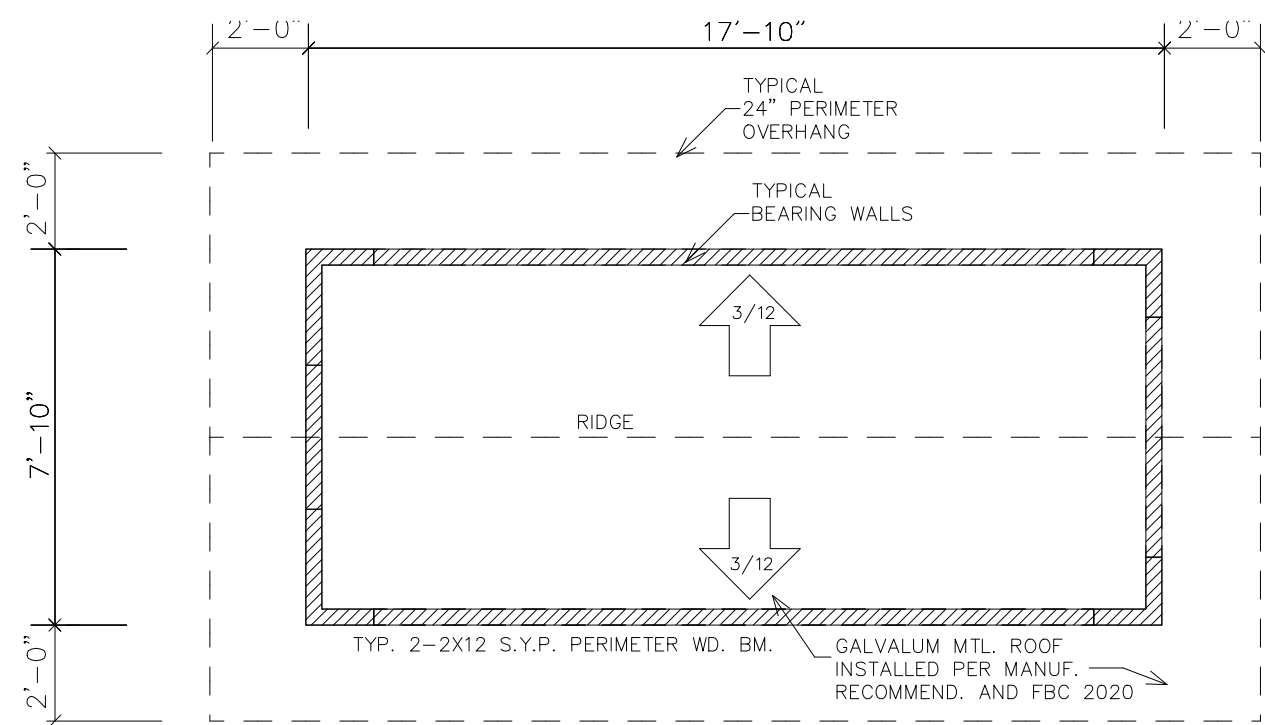

NEW OUTDOOR BAR ROOF PLAN


1/4"=1'-0"

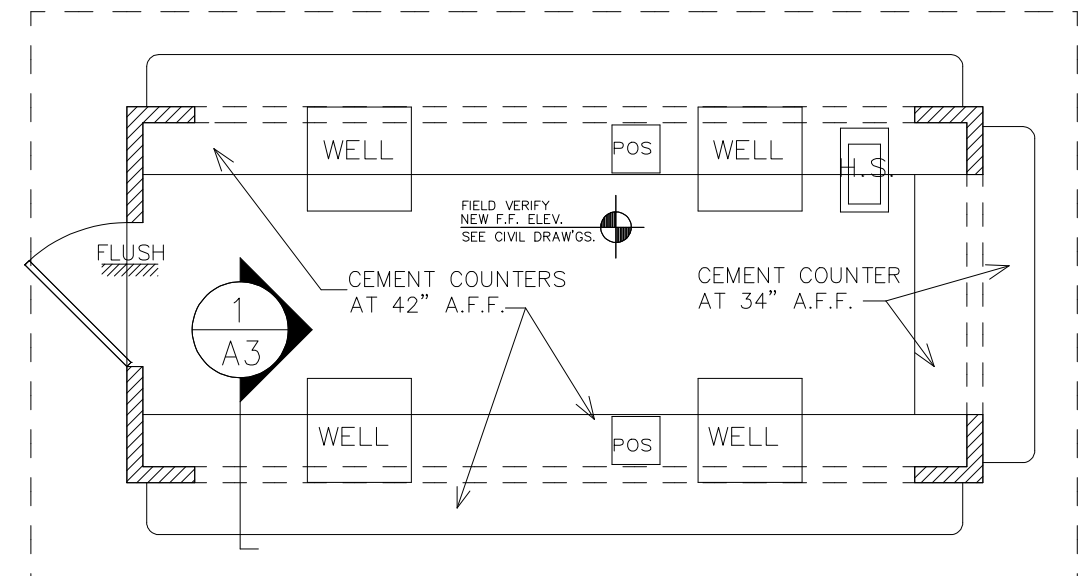

NEW OUTDOOR BAR FLOOR PLAN


1/4"=1'-0"

LEGEND
PERIMETER 16" MIN. LVL. WD. BMS. []
NEW 2X4 WD. WALLS []

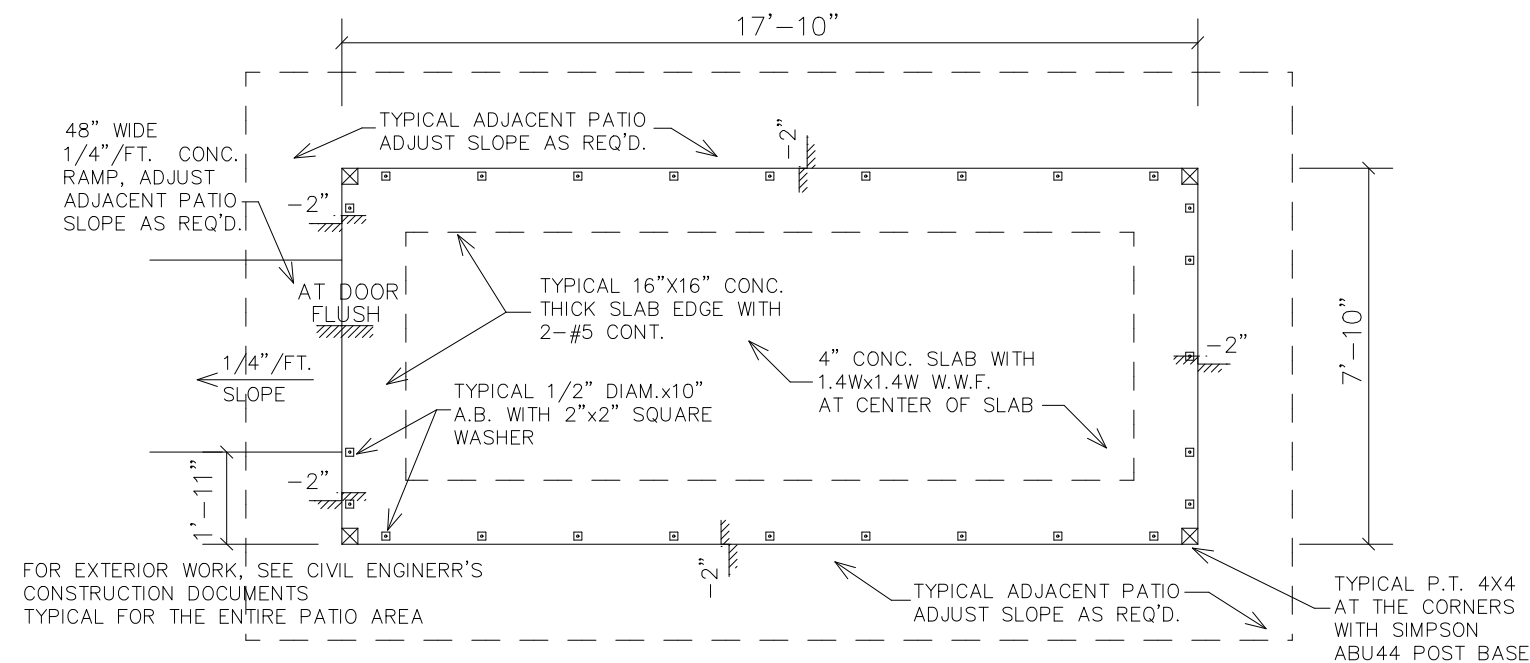


NEW OUTDOOR BAR FOUNDATION PLAN

1/4"=1'-0"

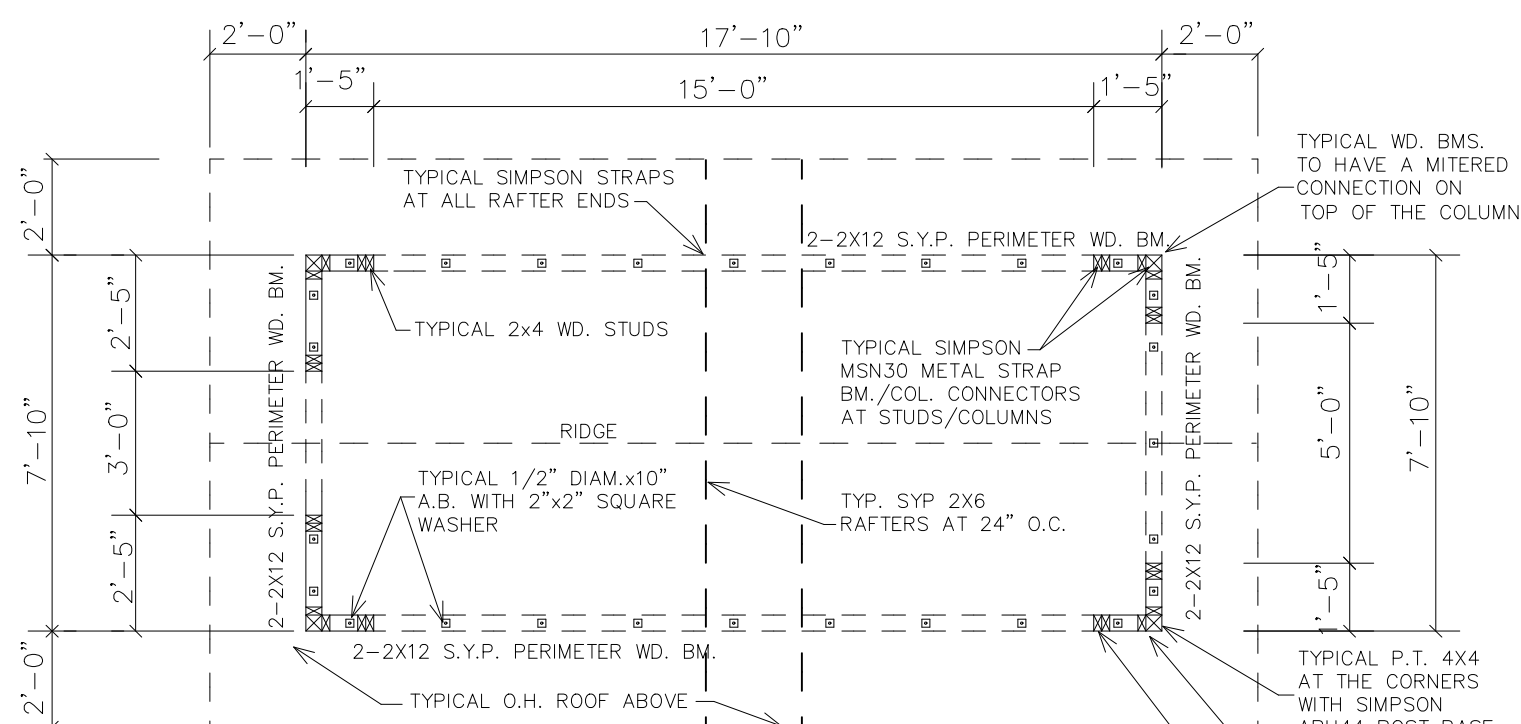


NEW OUTDOOR BAR UPLIFT PLAN

1/4"=1'-0"

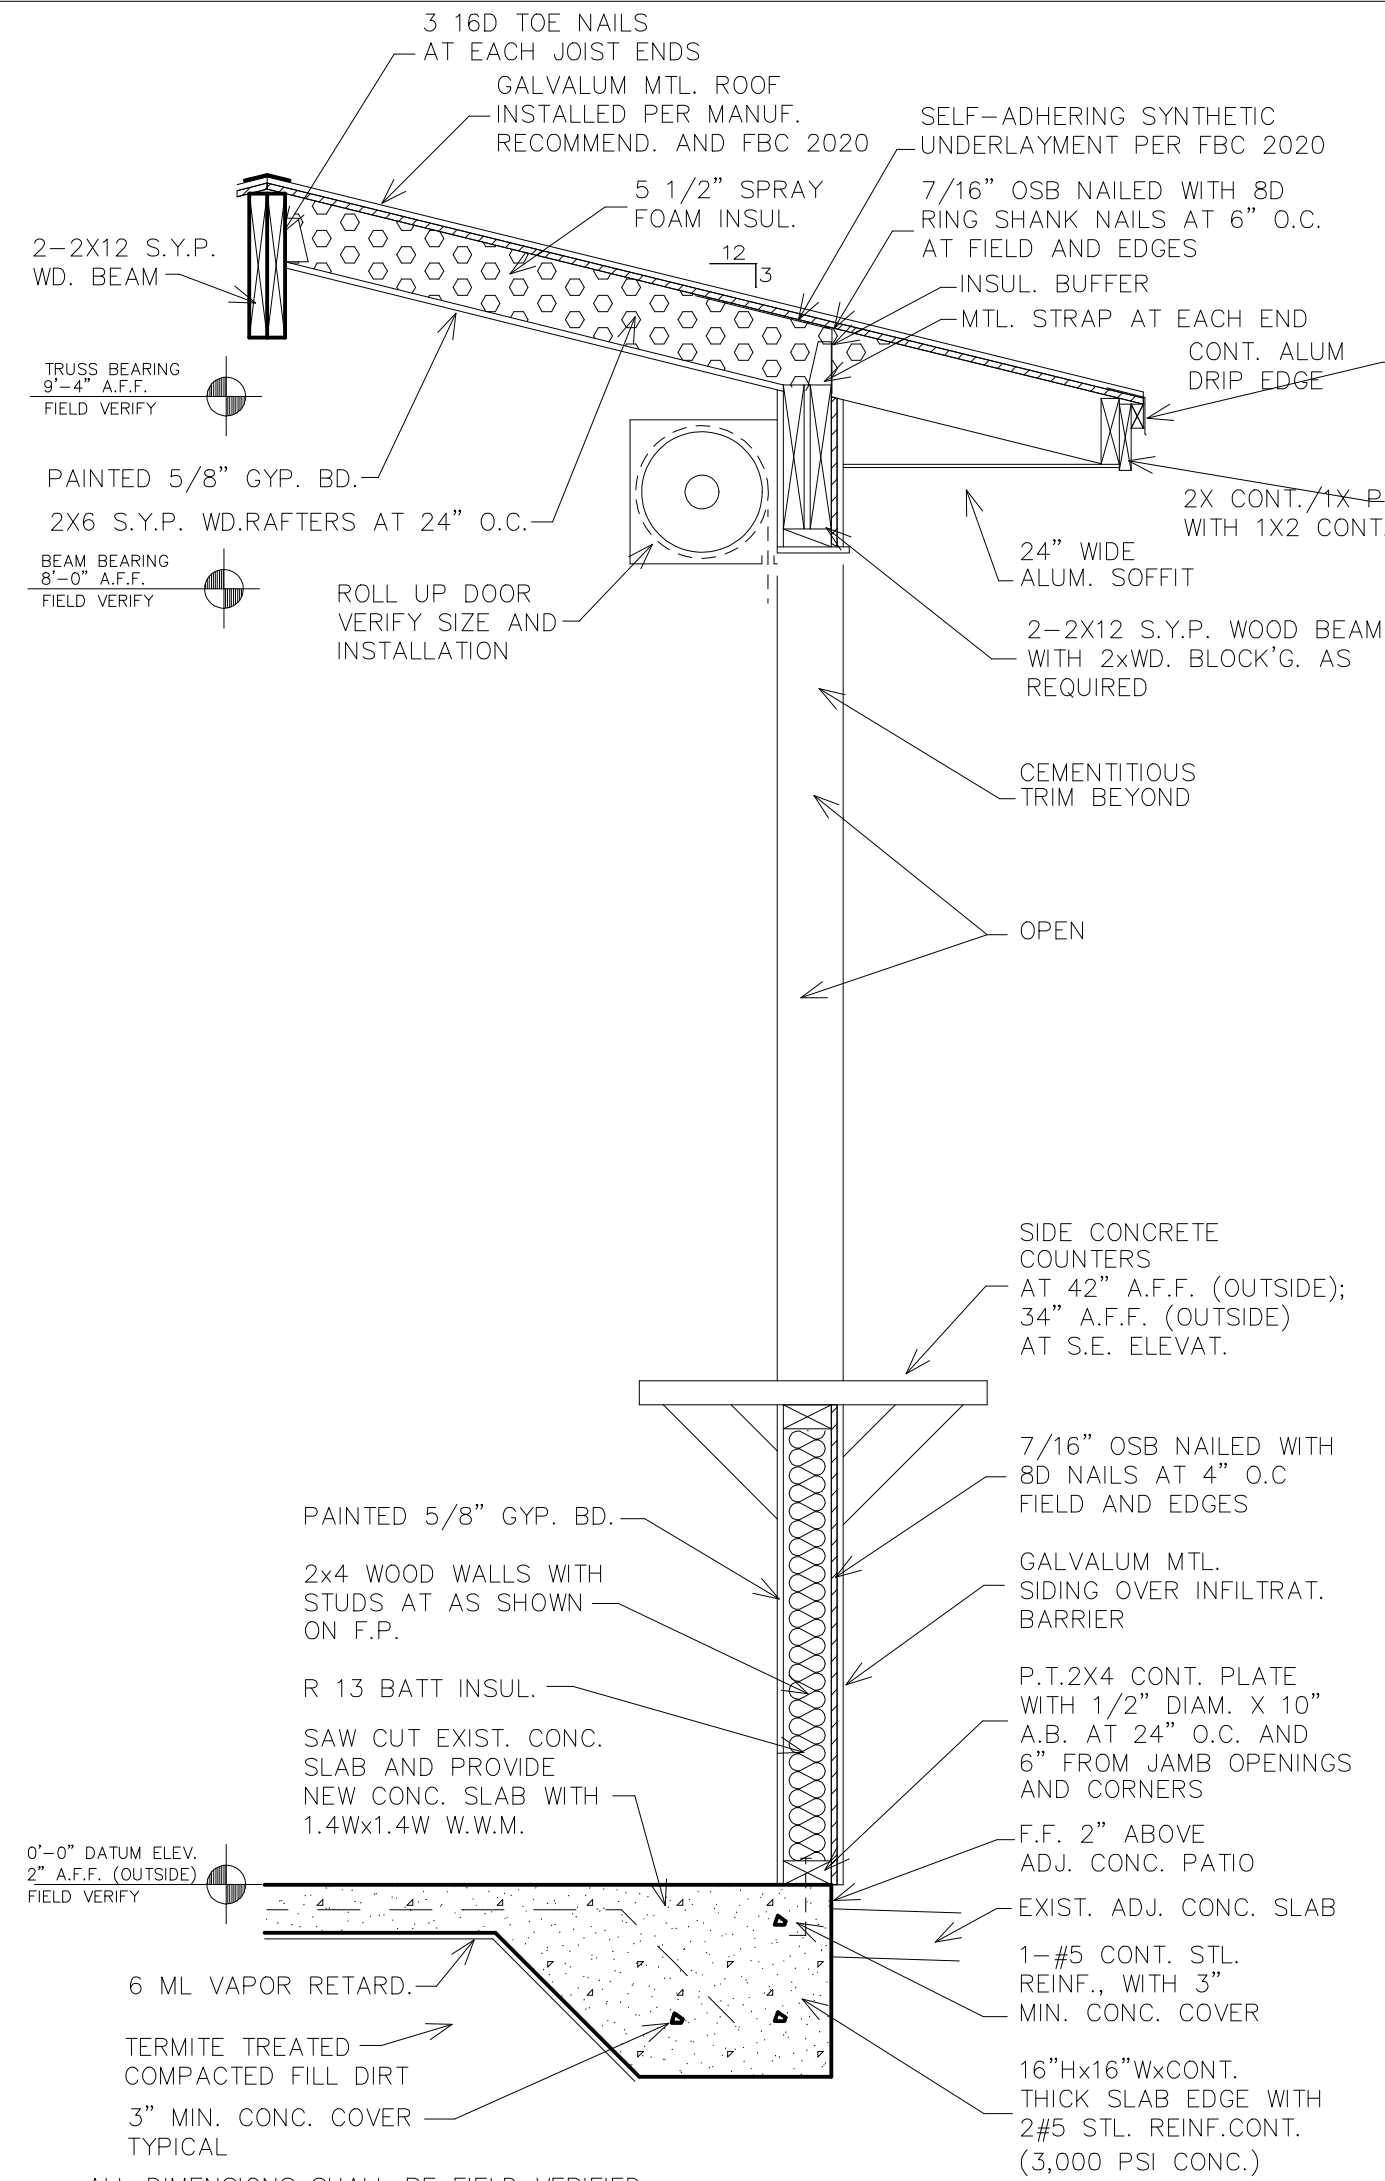


OUTDOOR BAR WALL SECTION DETAIL

3/4"=1'-0"
NEW CONSTRUCTION STRUCTURAL DESIGNS COMPLIES WITH CHAPTER 16 OF FBC 2020

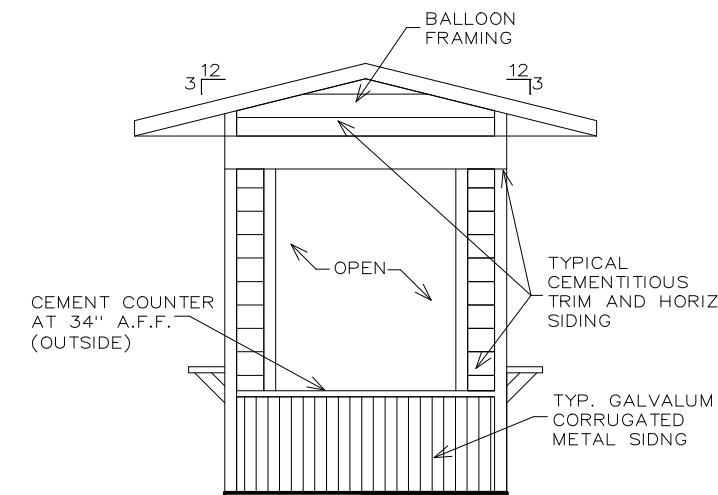


OUTDOOR BAR S.E. ELEVATION

1/4"=1'-0"

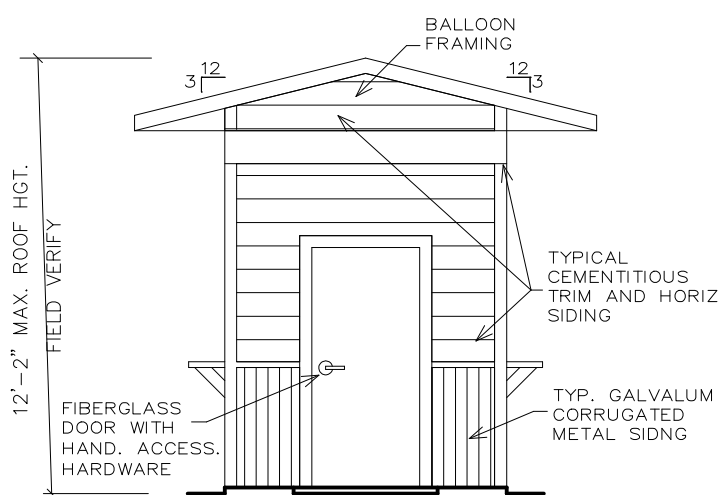

OUTDOOR BAR N.E. ELEVATION


1/4"=1'-0"

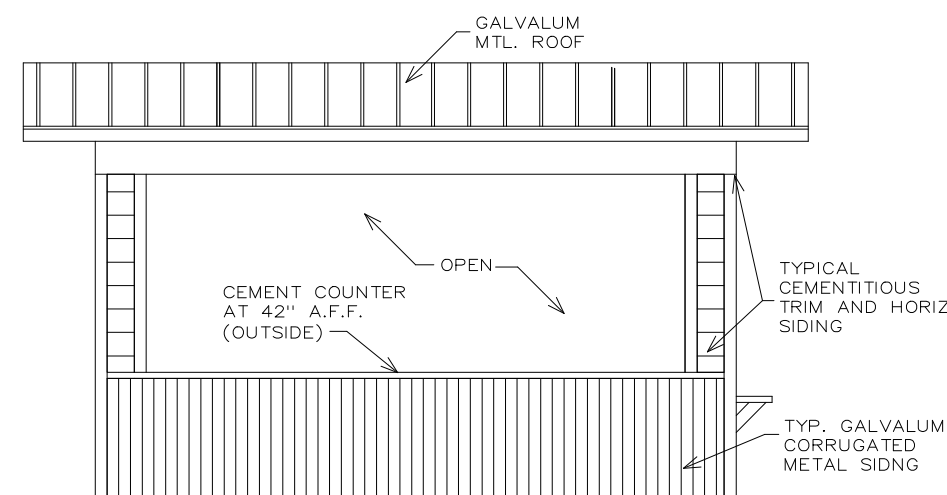

OUTDOOR BAR N.W. ELEVATION


1/4"=1'-0"

S.W. ELEV. SIMILAR

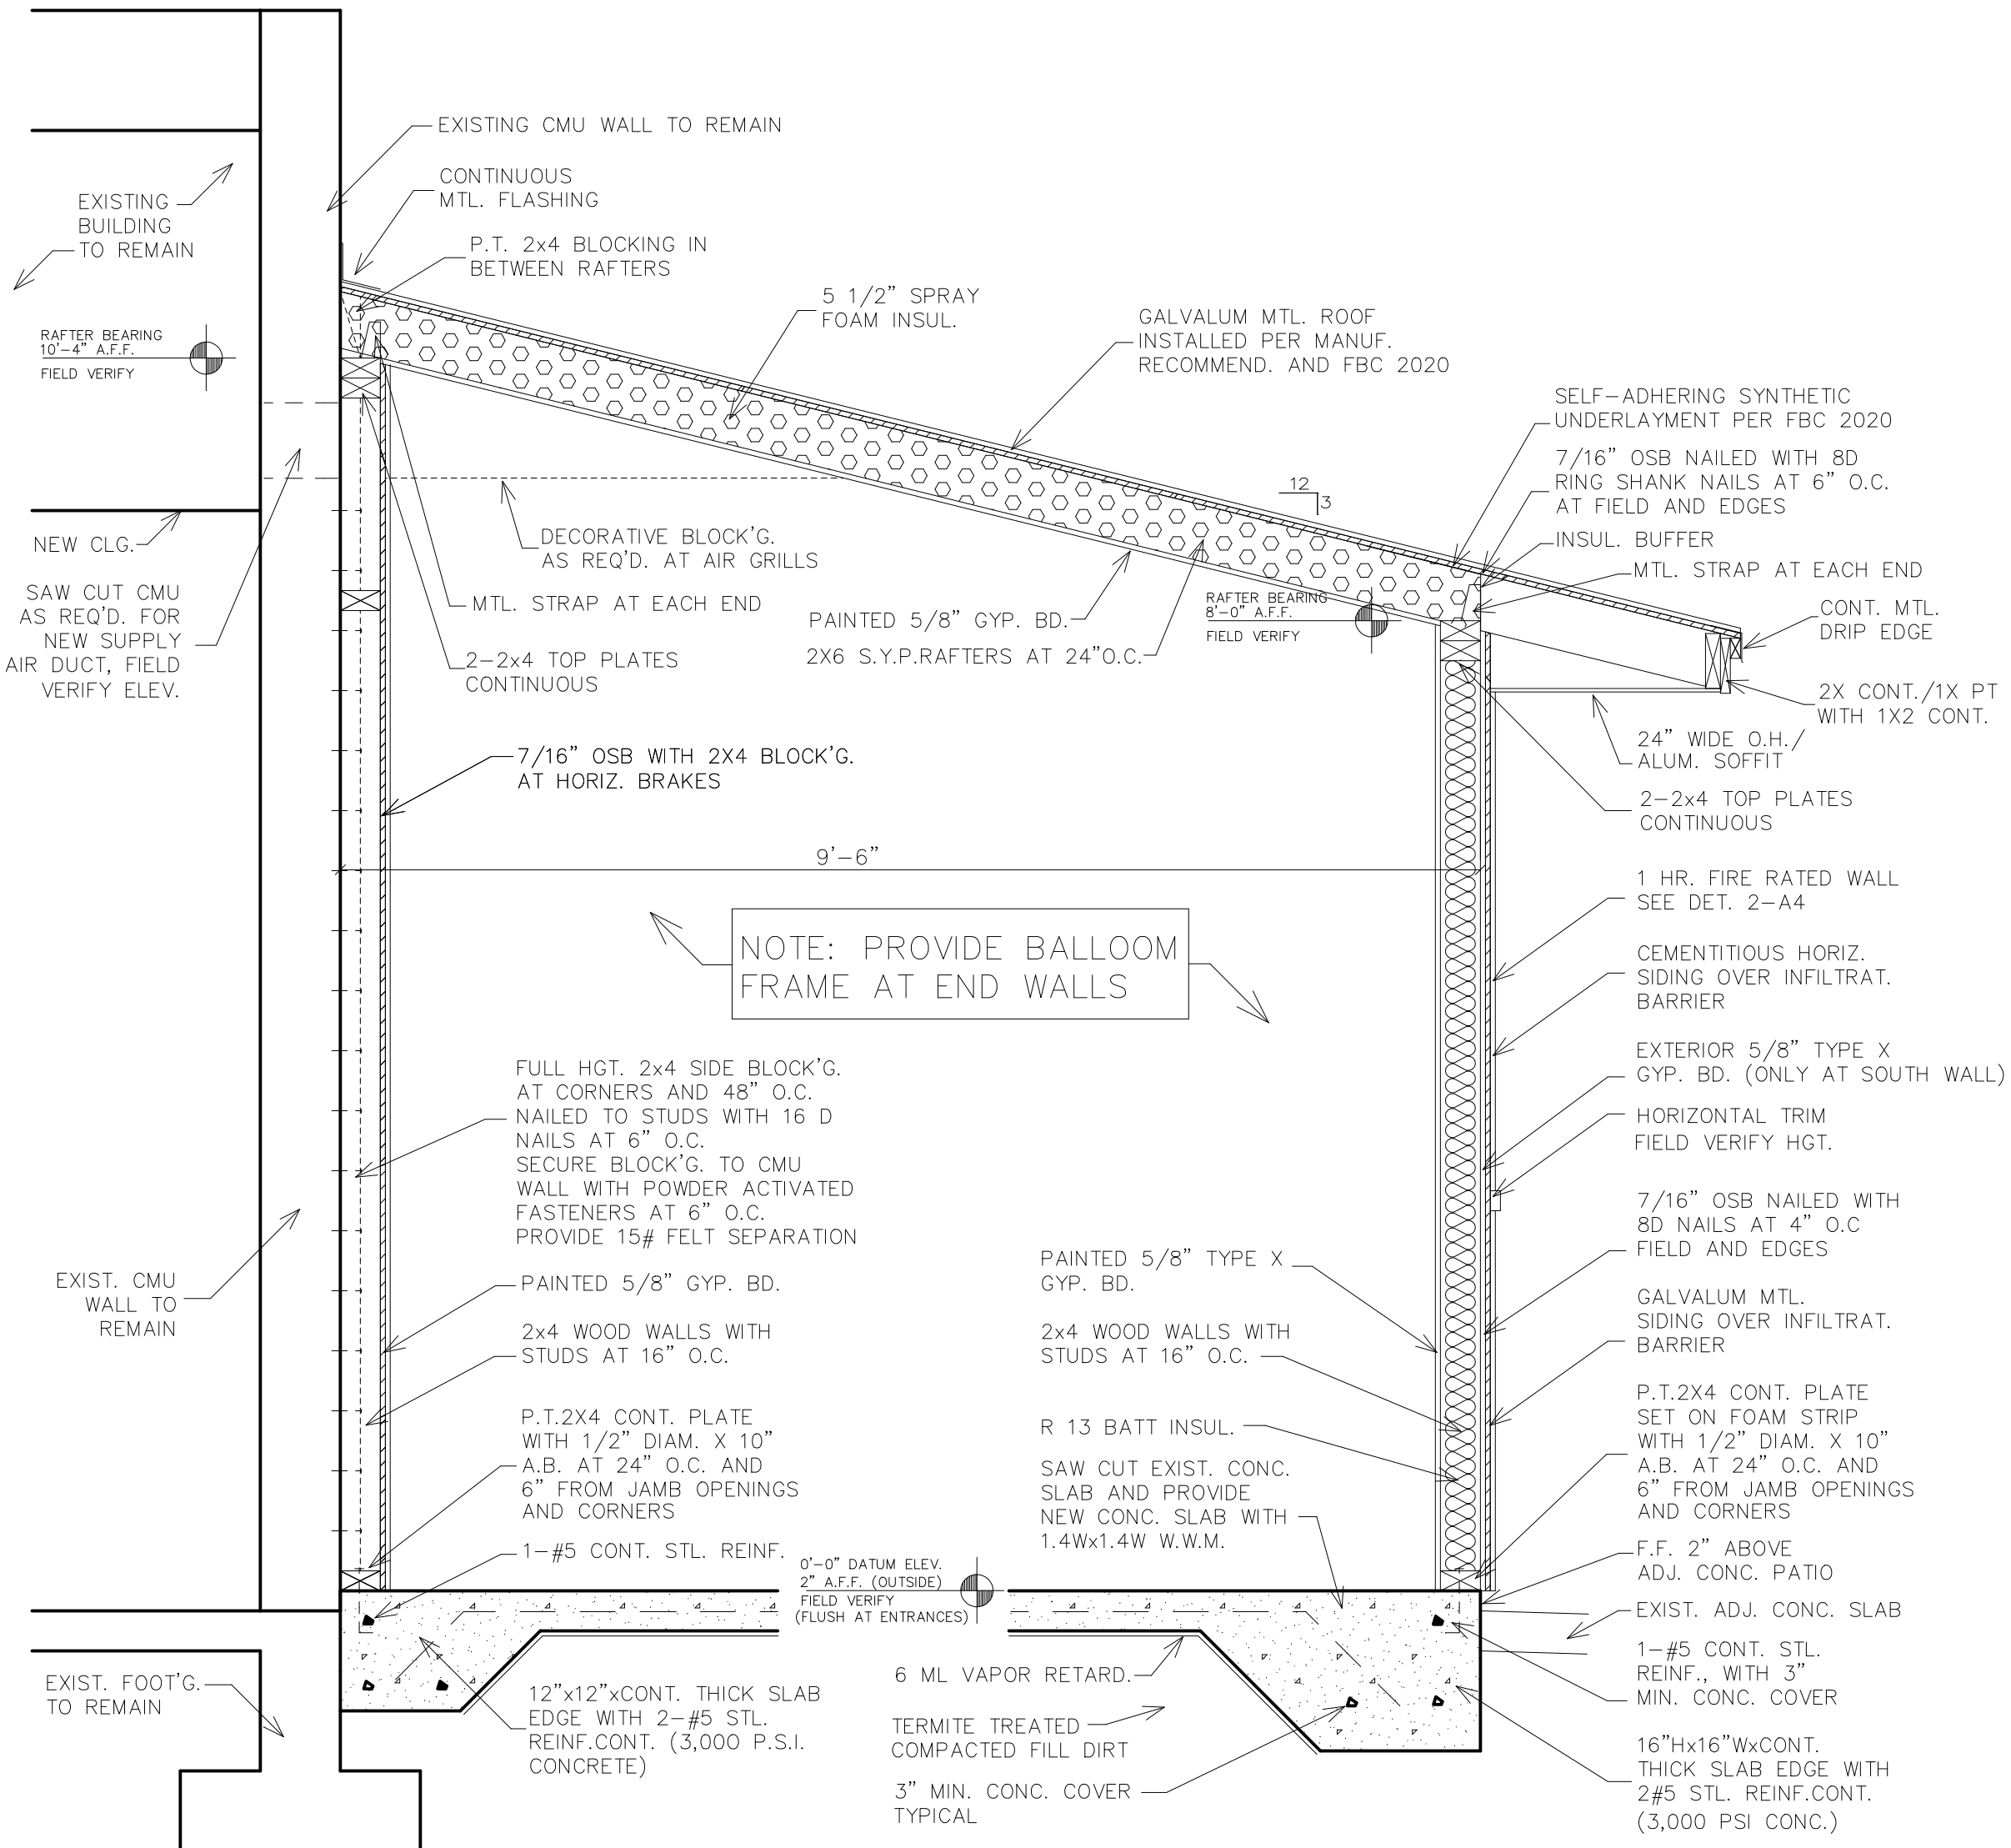


NEW WOMEN RESTROOMS WALL SECTION DETAIL

3/4"=1'-0"
NEW CONSTRUCTION STRUCTURAL DESIGNS COMPLIES WITH CHAPTER 16 OF FBC 2020

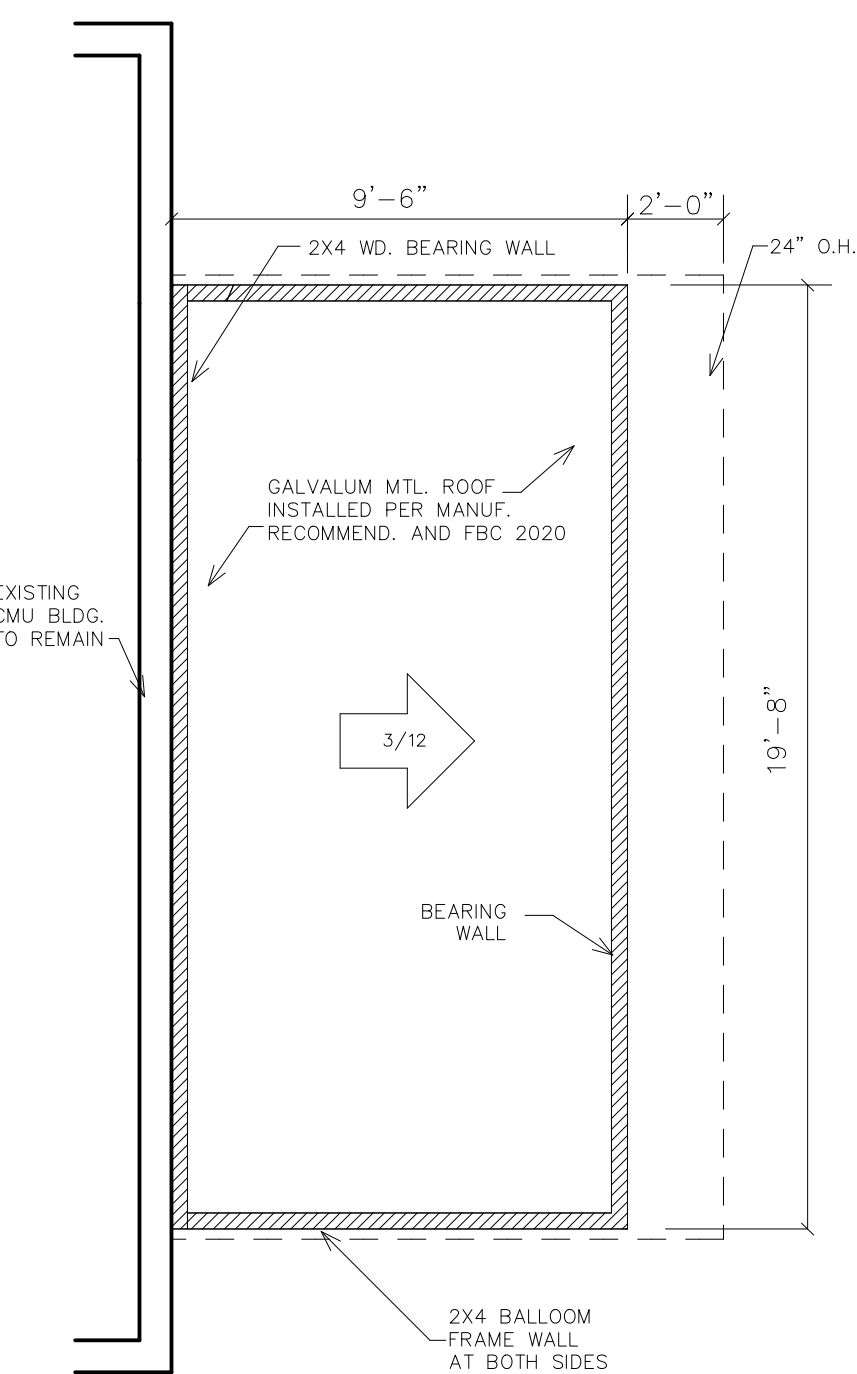


NEW WOMEN RESTROOM ROOF PLAN

1/4"=1'-0"

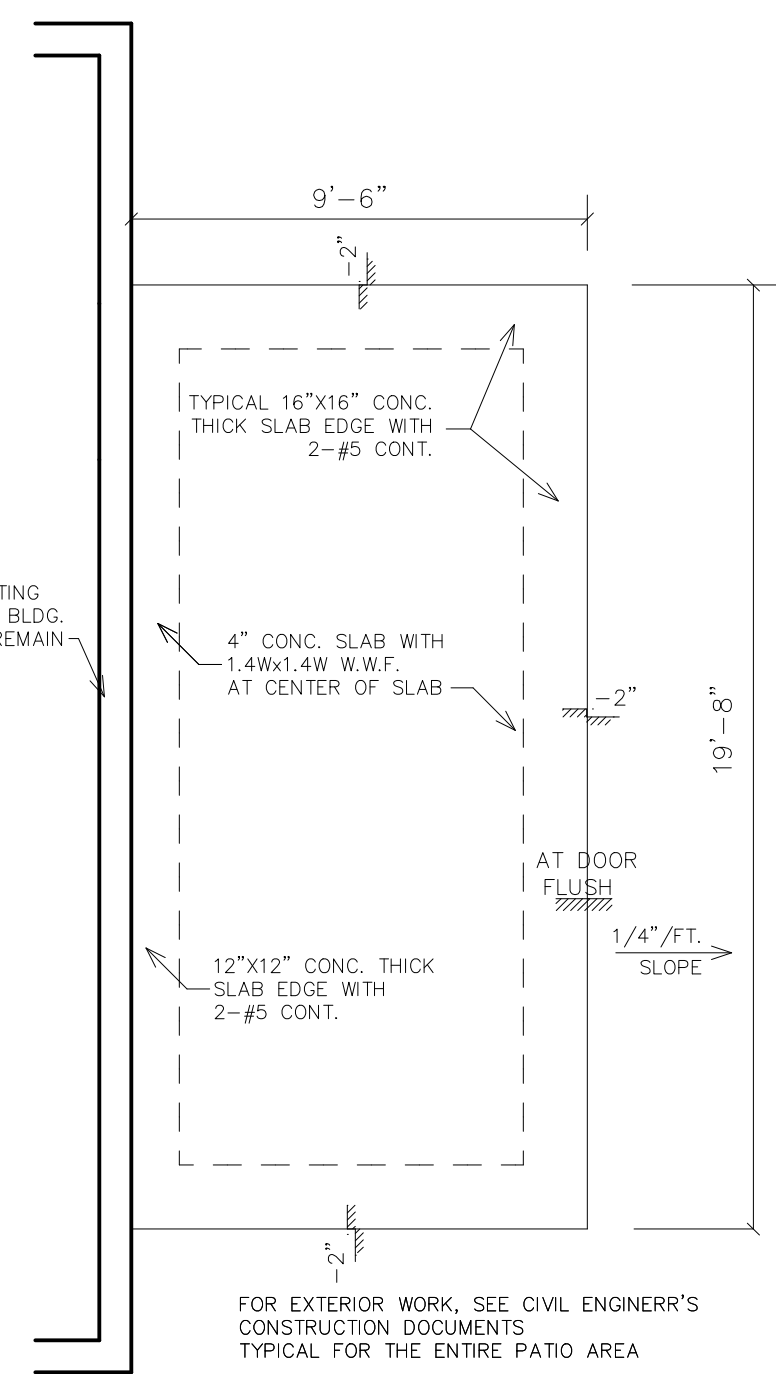


NEW WOMEN RESTROOM FOUNDATION PLAN

1/4"=1'-0"

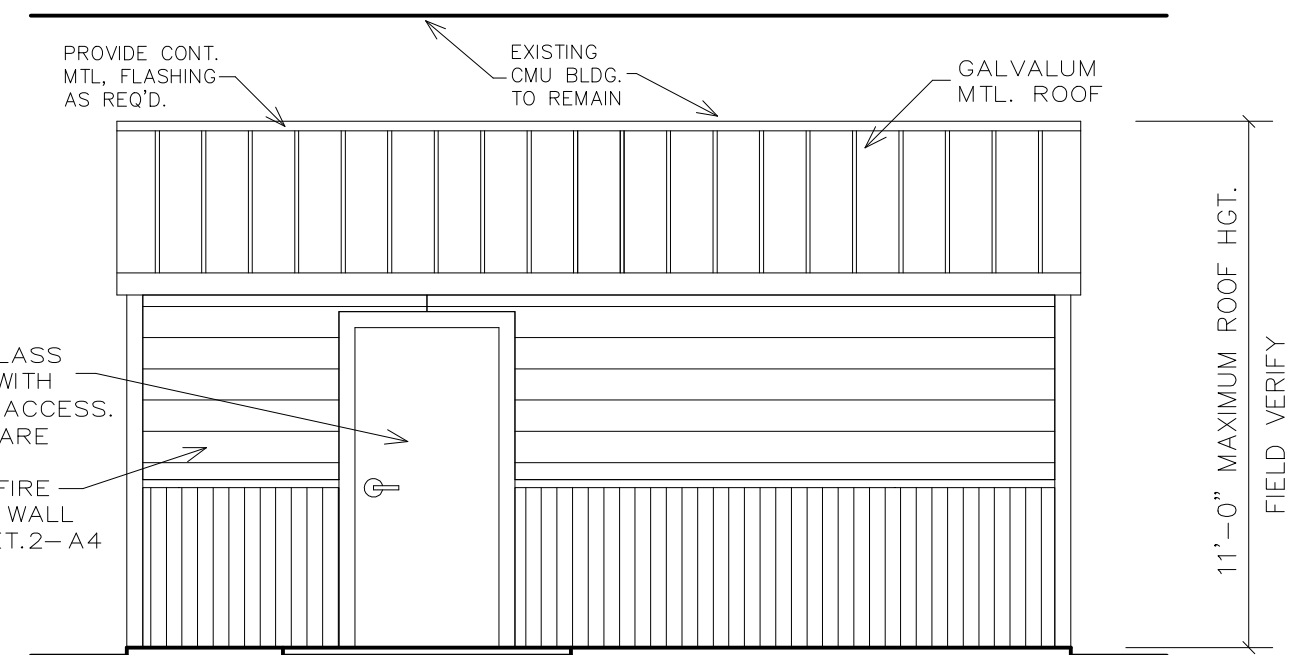

WOMEN RESTROOM SOUTH ELEVATION

1/4"=1'-0"

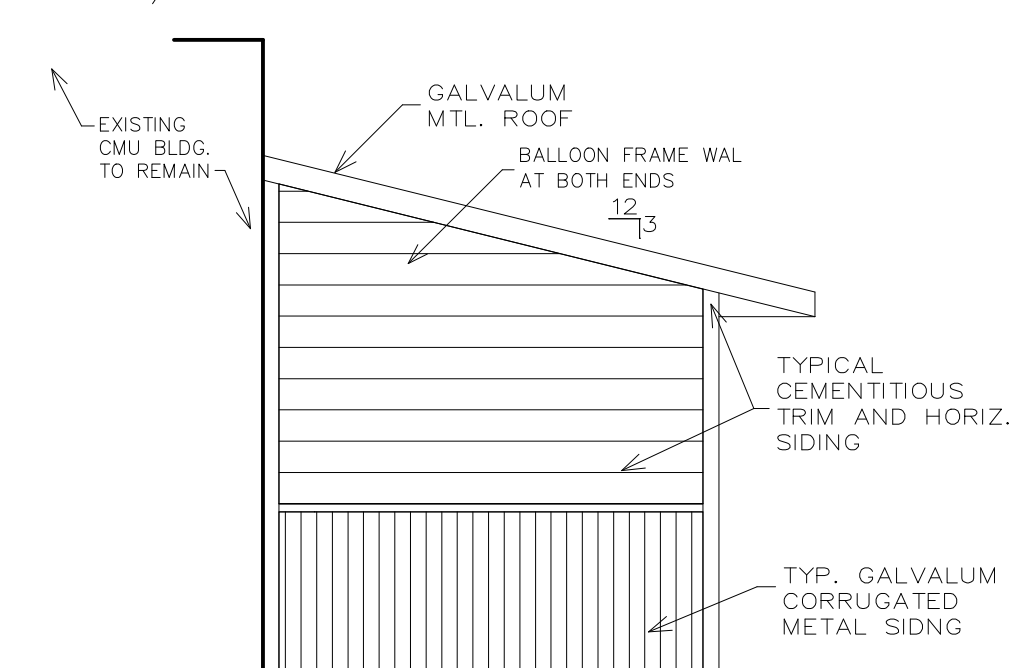

WOMEN RESTROOM WEST ELEVATION

1/4"=1'-0"

EAST ELEV. SIMILAR

RCA

RICARDO CAVALLINO
AND ASSOCIATES, INC.
ARCHITECTURE+PLANNING
AA 002865
352-377-1751
RCA@RCA22.COM
22 SE 5TH AVENUE
GAINESVILLE, FL 32601

RENOVATION OF EXISTING BAR AND OUTDOOR AREA
THE PALMS (PREVIOUS THE MIDNIGHT)
223 S. MAIN STREET, GAINESVILLE, FL

THIS DESIGN IS COPYRIGHTED
AND REMAINS THE PROPERTY
OF RICARDO CAVALLINO AND
ASSOCIATES, INC.
THIS DESIGN MAY NOT BE
USED FOR CONSTRUCTION,
PERMITTING OR OTHER USES
BY ANY PARTY UNLESS
WRITTEN PERMISSION IS
GRANTED BY R.C.A. INC.
UNAUTHORIZED USE OF THIS
DOCUMENT IS UNLAWFUL

PROJECT: RCA-20021
DRAWN BY: R.C.
CHECKED: N.N.
DATE: 9-24-2020

A3