
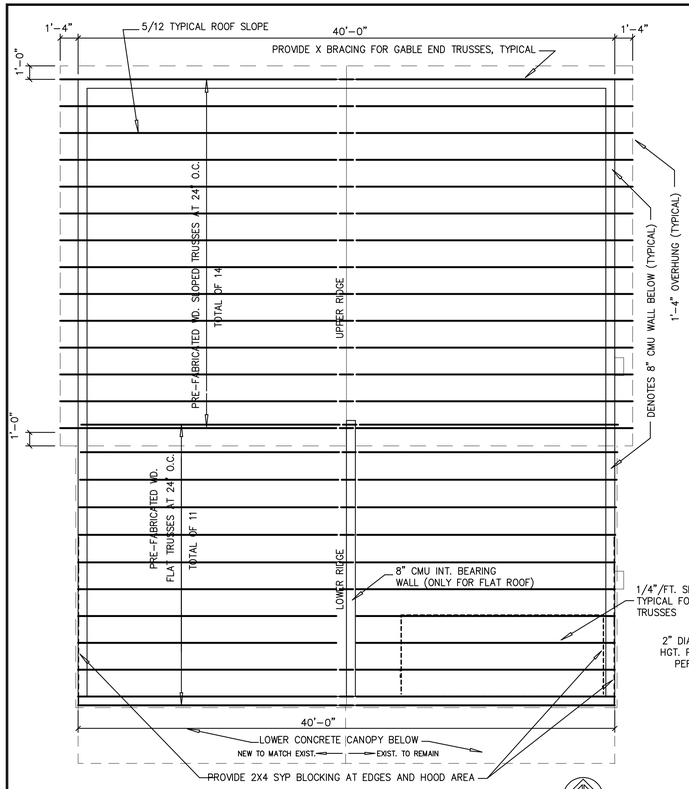



NEW ROOF FRAMING PLAN

3/16"=1'-0"

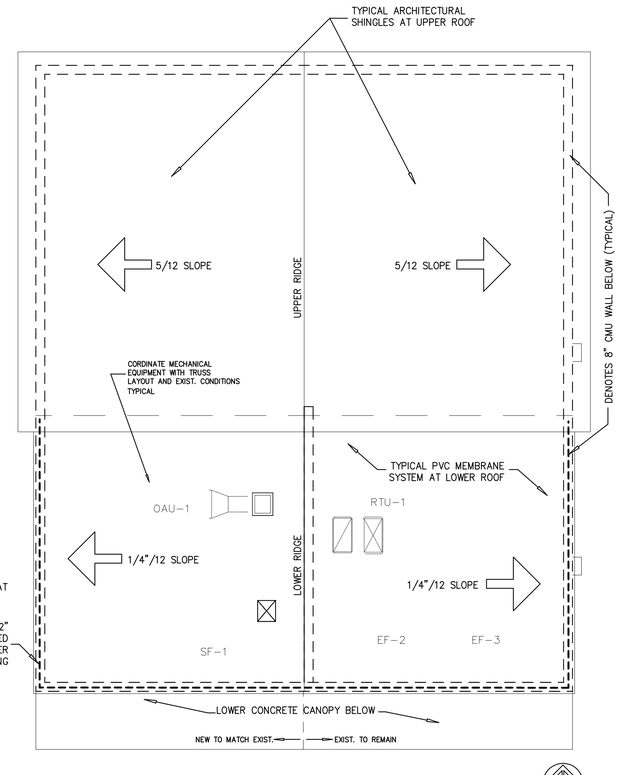

NEW ROOF PLAN


3/16"=1'-0"

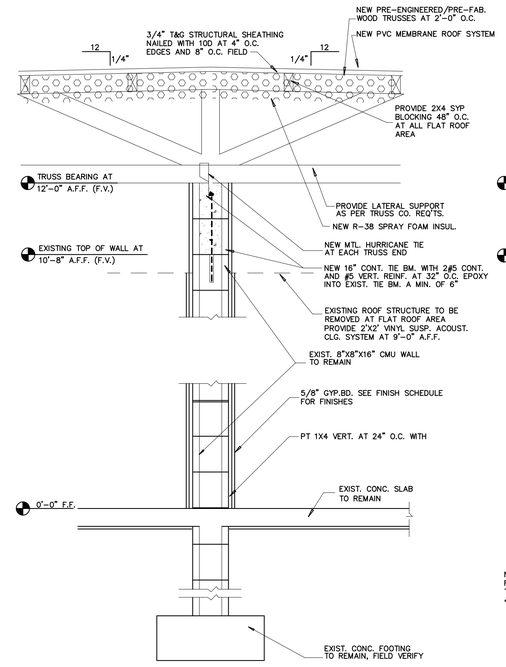

TYPICAL EXIST. INT. WALL SECTION

7/2


3/4"=1'-0"

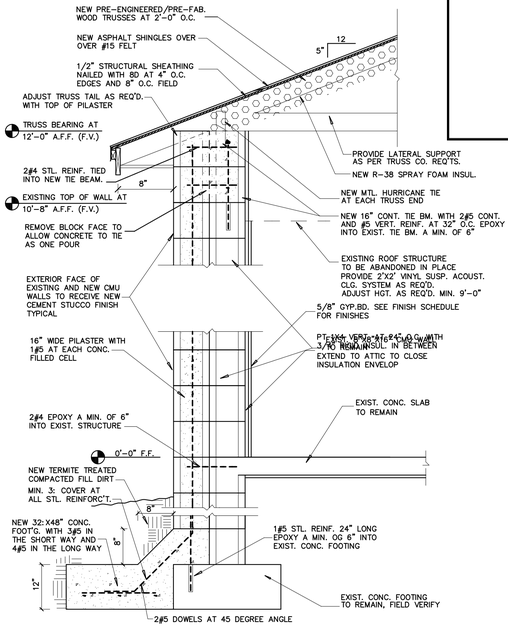

TYPICAL EXIST. WALL SECTION

6/2


3/4"=1'-0"

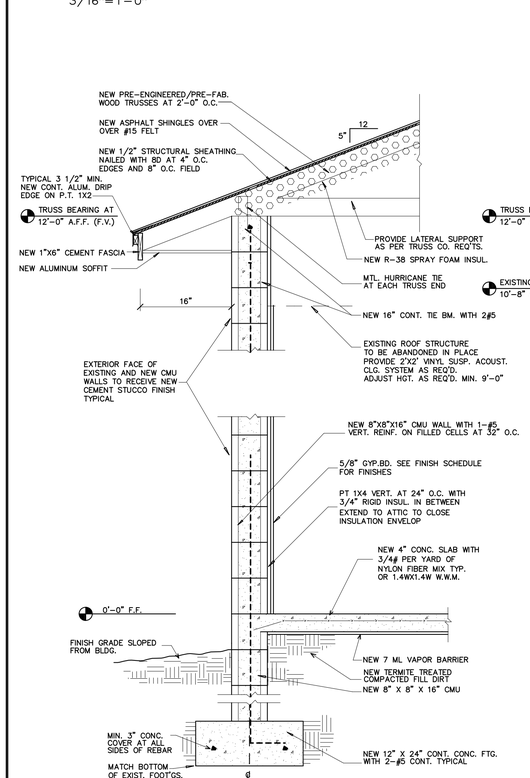

TYPICAL NEW WALL SECTION

1/2


3/4"=1'-0"

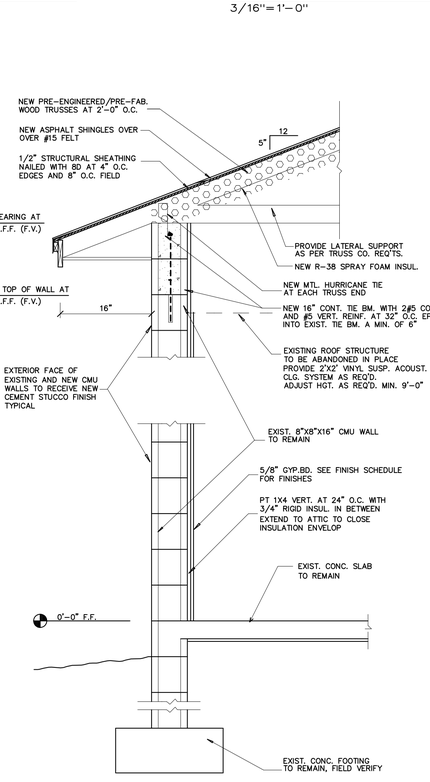

TYPICAL EXIST. WALL SECTION

2/2


3/4"=1'-0"

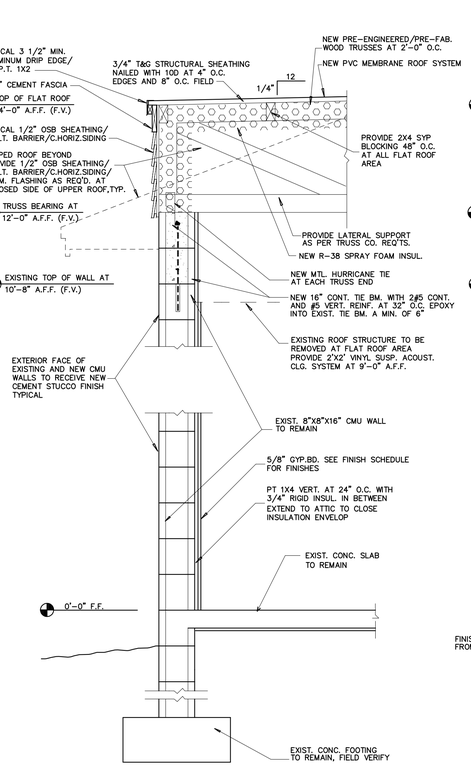

TYPICAL EXIST. WALL SECTION

3/2


3/4"=1'-0"

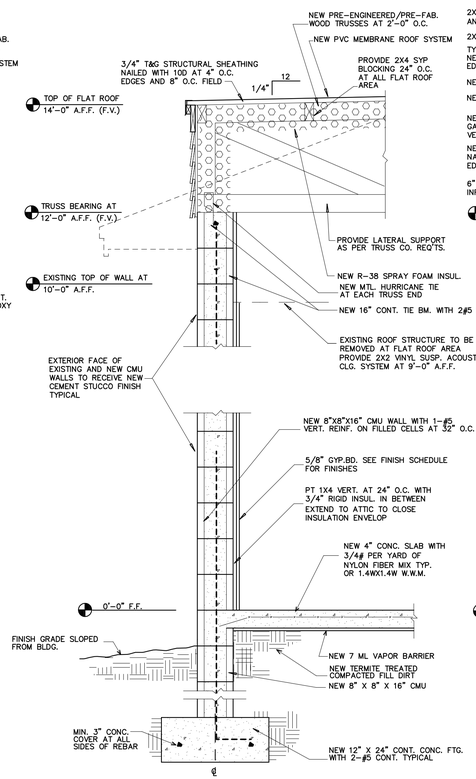

TYPICAL NEW WALL SECTION

4/2

3/4"=1'-0"

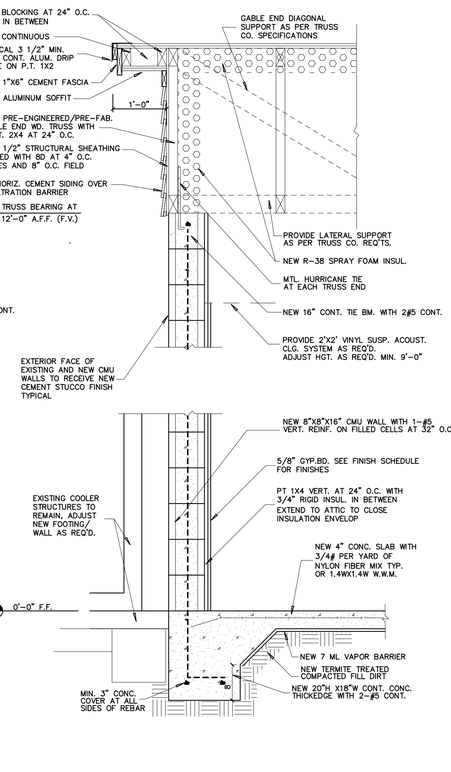

TYPICAL NEW WALL SECTION

5/2

3/4"=1'-0"

RICARDO CAVALLINO AND ASSOCIATES, INC
ARCHITECTURE—PLANNING AA 002865
22 SE 5TH AVENUE GAINESVILLE, FL 32601
352-377-1751 RCA@RCA22.COM

RENOVATION OF EXISTING FOOD TAKE OUT STORE TO SEAFOOD AND CHICKEN

GAINESVILLE SEAFOOD AND CHICKEN
2224 E. UNIVERSITY AVE., GAINESVILLE, FL

STATE OF FLORIDA RICARDO J.R. CAVALLINO --- AR0013032 REGISTERED ARCHITECT

THIS DESIGN IS COPYRIGHTED AND REMAINS THE PROPERTY OF RICARDO CAVALLINO AND ASSOCIATES, INC. THIS DESIGN MAY NOT BE USED FOR CONSTRUCTION, PERMITTING OR OTHER USES BY ANY PARTY UNLESS WRITTEN PERMISSION IS GRANTED BY R.C.A. INC. UNAUTHORIZED USE OF THIS DOCUMENT IS UNLAWFUL.

REVISED:

PROJECT: RCA-20020
DRAWN BY: R.C.
CHECKED: R.C.
DATE: 7-3-2020

A2